Lagern



NEUERO

SMART FARM TECHNOLOGIES

Inhaltsverzeichnis	Typ	Seite
Verkaufsmerkmale		3 - 4
Windschneelasten		5 - 6
Zubehör		7
Fundamente Zeichnungen		8 - 9
Belüftung Zeichnungen		10 - 11
Lagersilo Innenaufstellung	NLI	12 - 13
Lagersilo Außenaufstellung	NL 2 - 11	14 - 16
Lagersilo Außenaufstellung	NL 12 - 20	17 - 19
Lagersilo mit Konus	NLK	20 - 24
Lagersilo mit Trichter mit Stützen	NLT	25 - 27
Belüftungseinrichtungen		28 - 30
Ventilatoren	NV	31 - 40
Restentleerung	NFR, NFS, NFS HD	41 - 43
Laufstege, Aufstiegsleitern, Podeste		44 - 46
IGRAIN Temperaturmesssystem		47 - 48

Merkmale
NEUERO Lagersilos sind für die Lagerung von Schüttgütern z.B. wie Getreide ausgelegt und konstruiert.

Schüttgüter:
Schüttgüter werden bestimmt durch verschiedene Eigenschaften wie Korngröße (Körnung) und Kornverteilung, Schüttdichte, Rauheit, Feuchtigkeit und Temperatur. NEUERO Lagersilos sind geeignet für trockene freifließende (kohäsionslose) Schüttgüter, wie zum Beispiel:

Ackerbohnen	850 kg/m³	Maismehl	300 kg/m³
Bohnen	650 kg/m³	Malz, Trocken	500 kg/m³
Braugerste, nass	900 kg/m³	Malzmehl	630 kg/m³
Braugerste, trocken	550 kg/m³	Malzschrot	400 kg/m³
Buchweizen	650 kg/m³	Oelsaat	700 kg/m³
Buchweizenmehl	350 kg/m³	Oelsaatschrot	500 kg/m³
Erbsen	850 kg/m³	Raps	600 kg/m³
Erbsenkleie	250 kg/m³	Reis	750 kg/m³
Erbsenmehl	450 kg/m³	Reis, poliert	750 kg/m³
Fischmehl	750 kg/m³	Reis, rau	570 kg/m³
Futterkalk	1800 kg/m³	Reisflocken	210 kg/m³
Gerste (Brau)	720 kg/m³	Reishülsen	105 kg/m³
Gerste (Futter)	660 kg/m³	Reismehl	450 kg/m³
Gerstenkleie	250 kg/m³	Reisspelzen	120 kg/m³
Gerstenmehl	400 kg/m³	Roggen (Gebirgs)	700 kg/m³
Gerstenschrot	600 kg/m³	Roggenkleie, fein	380 kg/m³
Getreide	600 kg/m³	Roggenkele, grob	320 kg/m³
Grassamen	160 kg/m³	Roggenmehl	550 kg/m³
Hafer	500 kg/m³	Sojabohnen	700 kg/m³
Hafermehl	500 kg/m³	Sojamehl	420 kg/m³
Haferschälkleie	350 kg/m³	Sojaschrot	550 kg/m³
Hirse (Milokorn)	800 kg/m³	Sonnenblumenkerne	350 kg/m³
Hirsemehl	450 kg/m³	Weizen, hart	850 kg/m³
Kleie	300 kg/m³	Weizen, weich	780 kg/m³
Linsen	850 kg/m³	Weizenkleie, fein	350 kg/m³
Mais, grobkörnig	800 kg/m³	Weizenkleie, grob	250 kg/m³
Mais, kleinkörnig	880 kg/m³	Weizenmehl (405-630)	600 kg/m³
Maisgrieß	650 kg/m³	Weizenschrot, fein	600 kg/m³
Maisklebermehl	500 kg/m³	Weizenschrot, grob	520 kg/m³
Maiskleie	300 kg/m³		

Freifließende Schüttgüter sind problemlos mit geeigneter Fördertechnik auszutragen.

Technische Merkmale:


Statische Grundlage	: Silozylinder, Silodach und Fundament nach EUROCODE DIN EN 1991 und DIN EN 1993
Erdbebenzone	: UBC-Zone-O; Ao: 0,0g
Silodach Schneelast	: 100 kg/m² im Standard
Windgeschwindigkeit	: 90 km/h im Standard
Silo Mantelplatten	: 600 gr/m² xxx verzinkt; 42 µ/m² +/- Toleranz
	: 275 gr/m², FVZ S350 GD-Z275-MA, VS Polyester 25µ
	: Güte: SQ-Grade 340 / St E350-GD
	: Wellung Schritt 120mm x 9 mm
Glanzgrad	: 30 +/- Glanzeinheit, RAL 5005 gem. Farbmuster 4085 mit Schutzfolie
Silodachausführung	: Aluzink-Beschichtung AZ 185
Schrauben	: M10 8.8 FVZ
Density Design Parameter	: 830 kg/m³
Verankerungsmaterial	: je Platte 2x 20/330 AG RGM
	: Stärke 25 mm FVZ

Verkaufsmerkmale

- Herstellung in Deutschland (einziger in Deutschland produzierender Silohersteller) – jahrzehntelange Erfahrungen im Silobau
- Auslegung und Bereitstellung einer Typenstatik für Silo und Fundament nach EUROCODE für NL 2 - 11
- Kurze Lieferzeit durch Eigenfertigung
- Gewalzte Qualitätsstahlbleche mit Herstellerprüfbescheinigung
- Flache Wellung des Silobleches, dadurch geringer Reinigungsaufwand an der Silowandung
- Mantelplatten, Schrauben und Stützen mit hoher Verzinkungsgüte, dadurch lange Lebensdauer
- Wellenberg und Wellental doppelt verschraubt, dadurch hohe Stabilität und sichere Tragkraft der Gewichte von Laufsteg, Leitern und Podesten
- Geringer Abstand der Verschraubungen im horizontalen Bereich, dadurch hohe Standfestigkeit
- Verzinkte C-Profilstützen bis Zylinderoberkante nach statischen Vorgaben
- Rostfreie Bodenanker
- 30° Silodächer mit Aluzink-Beschichtung, stabile leichte Ausführung mit langer Lebensdauer
- Eigenfertigung von Zubehörteilen und dadurch individuelle Ausführungen lieferbar
- Vorschlag für wetterfeste und optimierte Fundamente

Optionale Ausführungen

- Silozylinder und Silodach auf Wunsch in allen gängigen RAL-Farben lieferbar
- Individuelle Lösungen für Sonderwünsche, z.B. bei höheren Schneelasten, Windlasten etc.
- Individuelle Lösungen für Druckentlastungseinrichtungen, z.B. bei Pelletsilos mit Kunststoffschrauben im Dach
- NEUERO integriert und liefert auf Wunsch alle Beschickungs- und Entnahmetechniken
- Einbau von Belüftungstechniken, Belüftungsböden, Belüftungskanälen
- Einbau von Temperatur-, Feuchtigkeits- sowie CO2-Überwachungstechnik einschließlich Steuerung, Dokumentation und Analyseprogrammen zur Qualitätssicherung und Überwachung

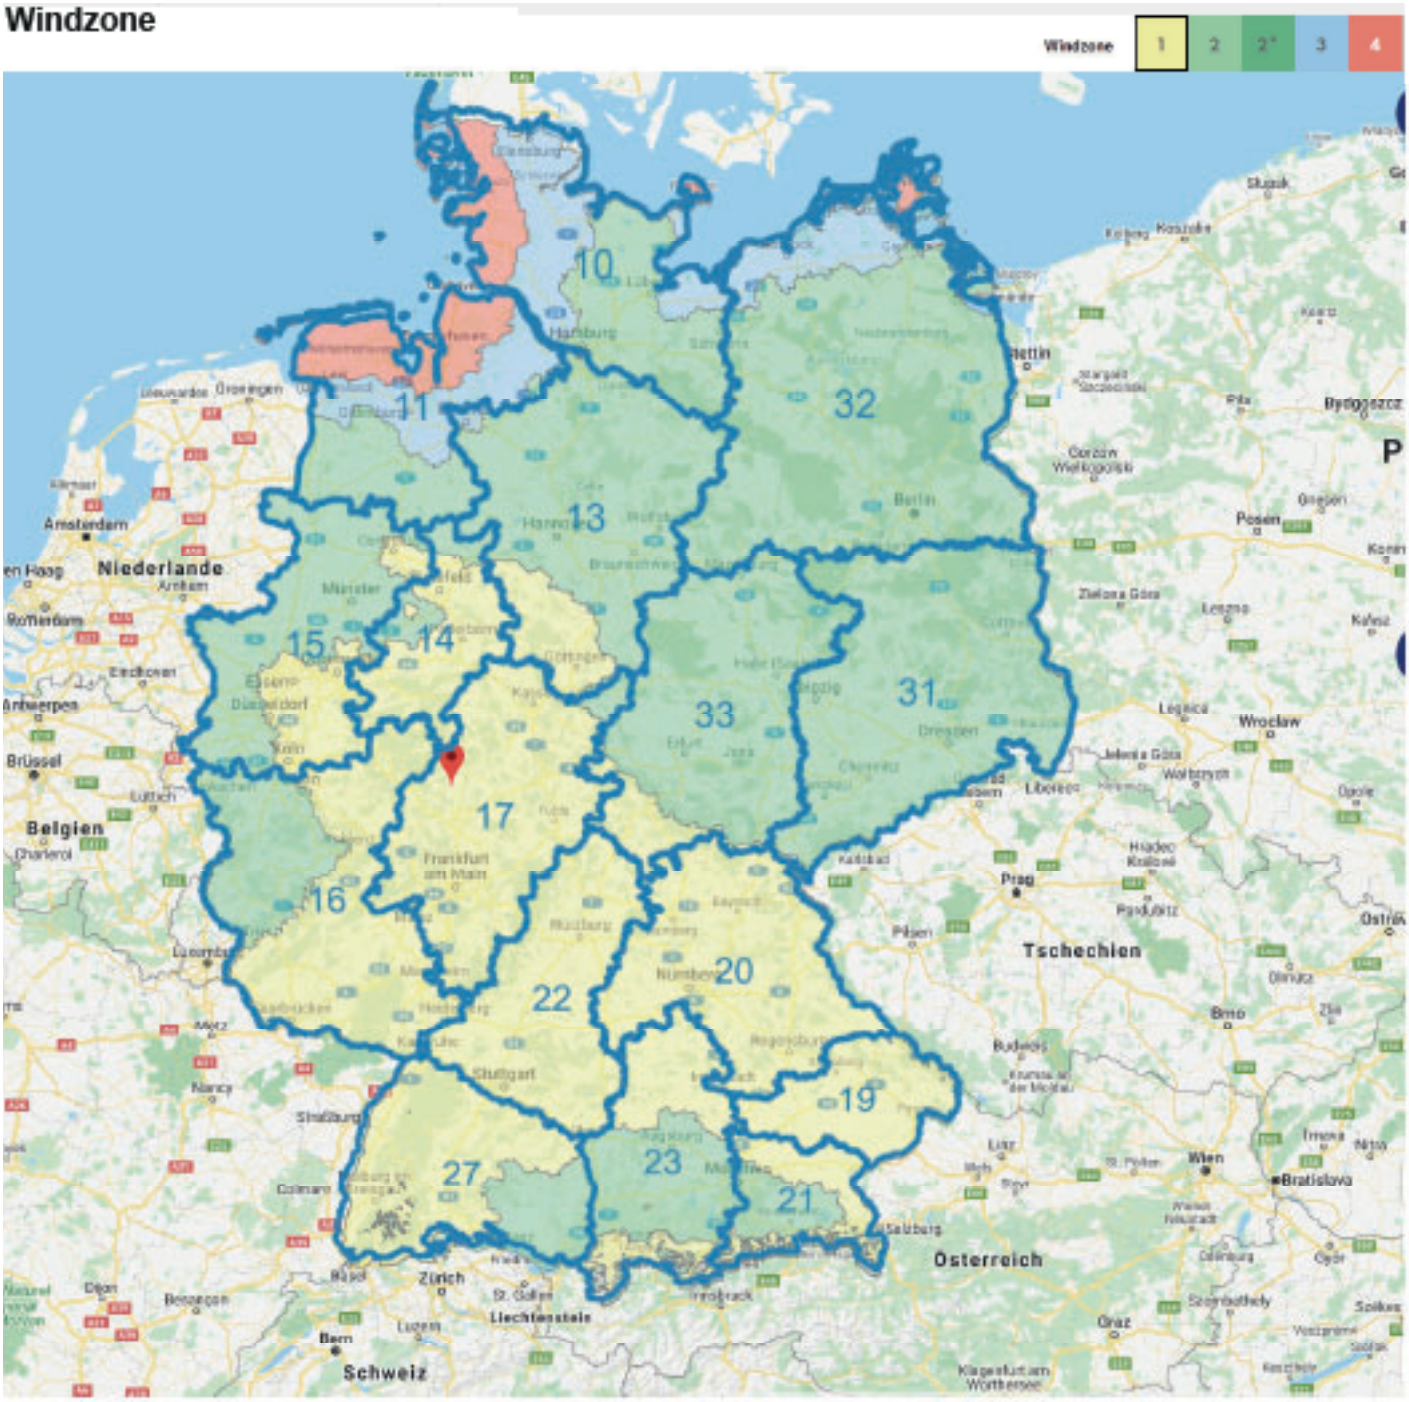


Links

Höhenkarte
https://de-de.topographic-map.com/places/gi/Deutschland/

Windlast-, Schneelast-, Erdbebenzonen
https://www.dlubal.com/de/loesungen/online-dienste/schnee-wind-erdbeben-lastzonen


Schneelastzonen

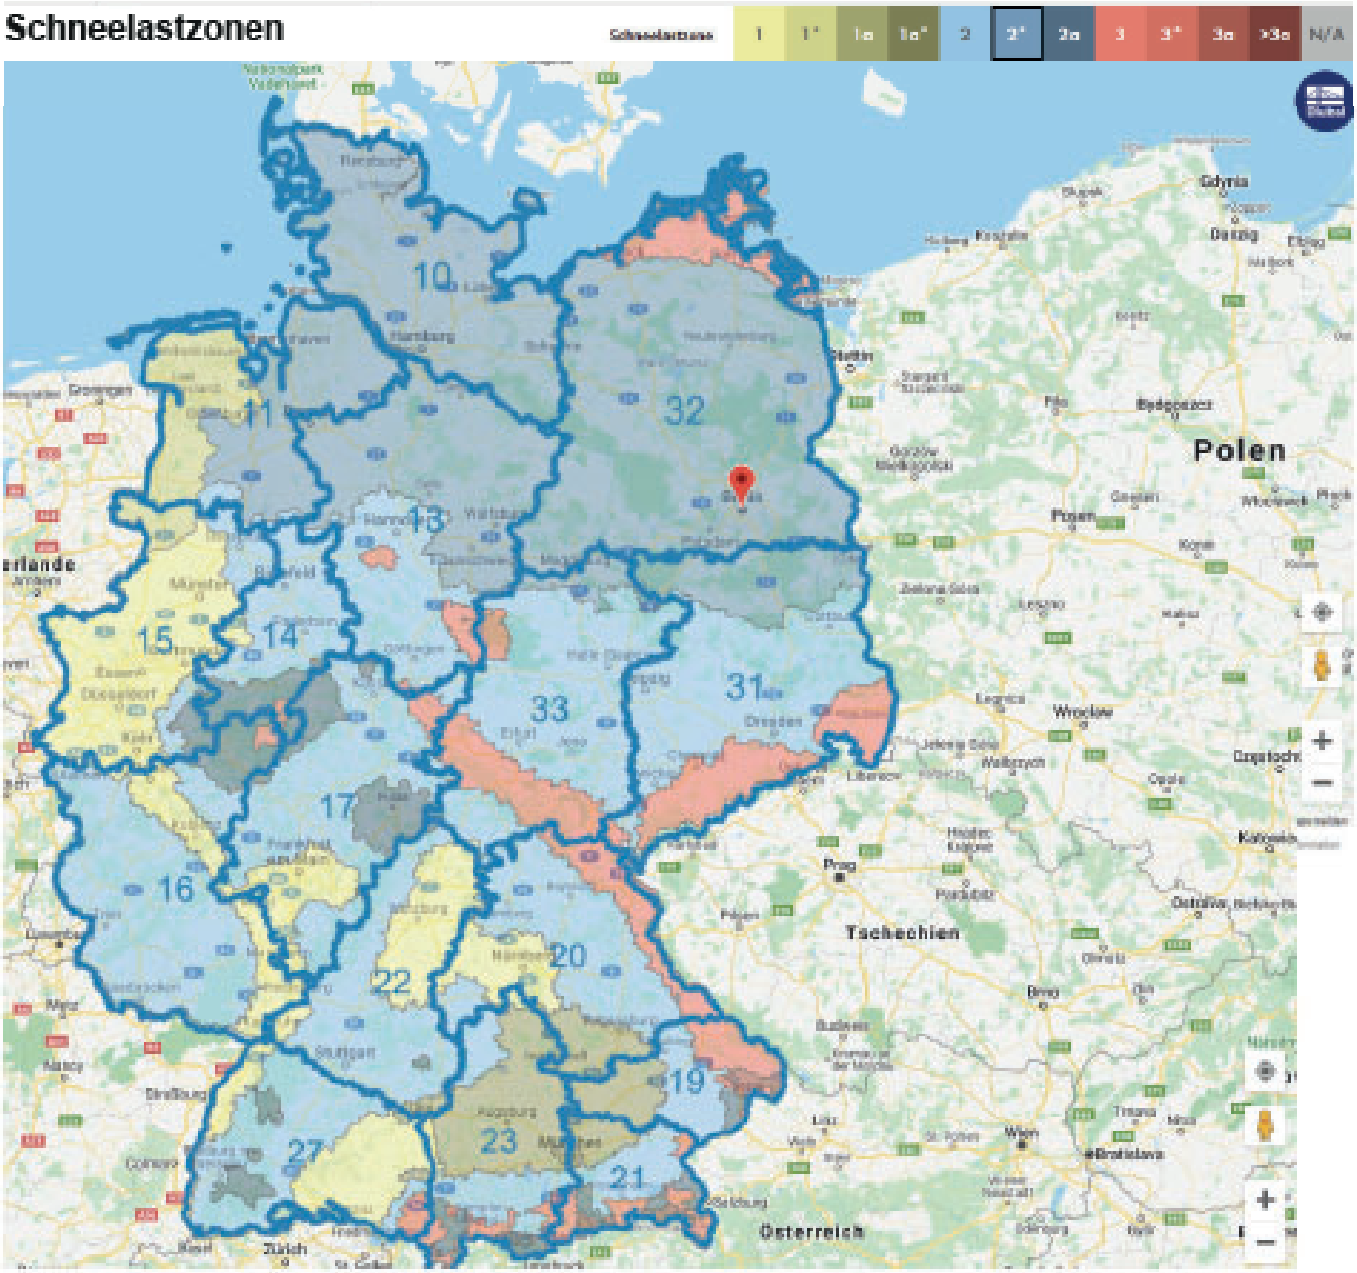


Erbebenzone




Zubehör

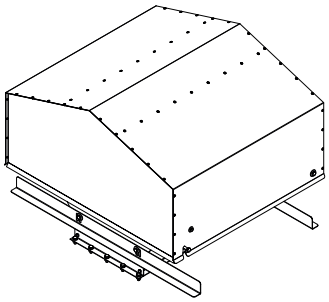


Dachentlüftungsgebläse NDE

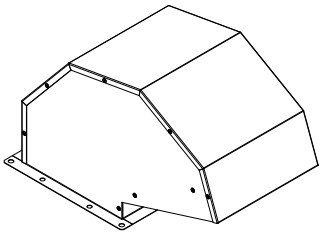


Entlüftungshaube 300x300

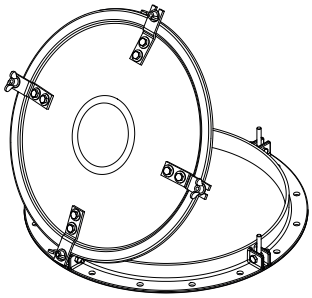


Dachluke Gr.560

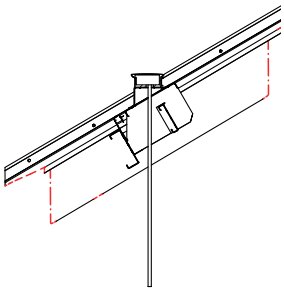


Messgehänge

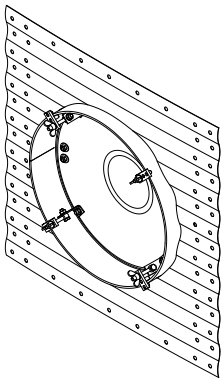


Einstiegsluke Ø560 kpl. für NL3-16

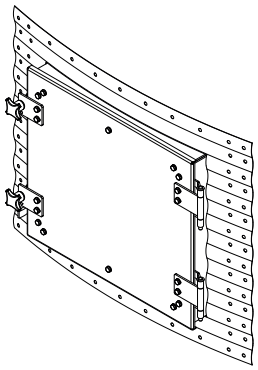


Einstiegsluke eckig NL3-NL22 (einfacher Stützenabstand)

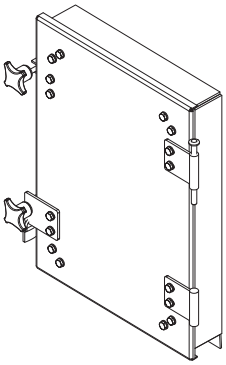


Einstiegsluke doppelte Stützenreihe

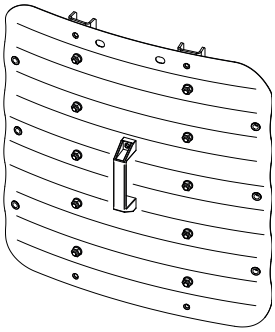


NLI Einstiegtür

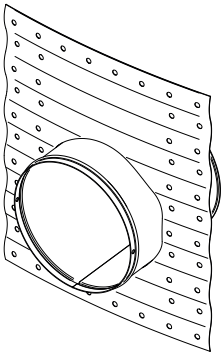


Siloanschlusstutzen

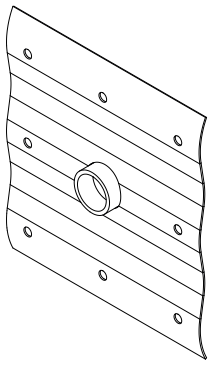


Einbaustutzen Drehflügelmelder am Silozylinder

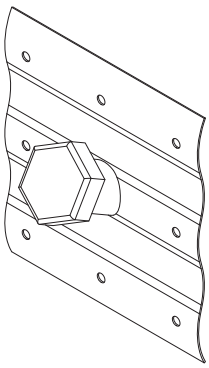

Messstutzen

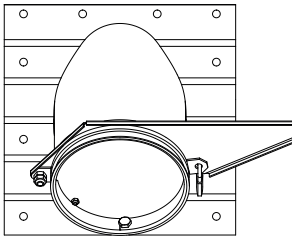



Notauslauf Gr.200 45° kpl.

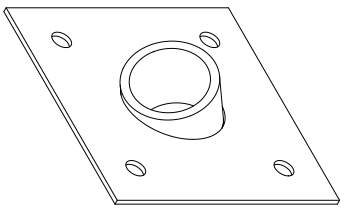


Einbaustutzen für Drehflügelmelder in Silodach 30°


B-B (1 : 25)

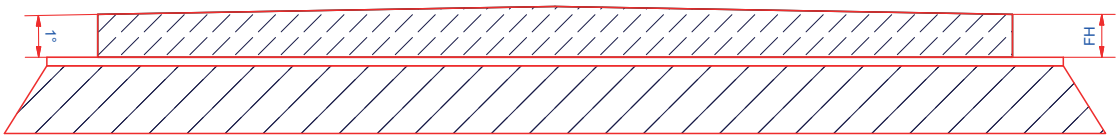


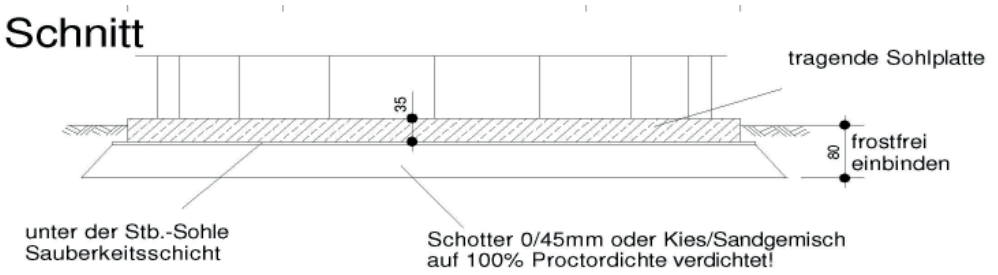


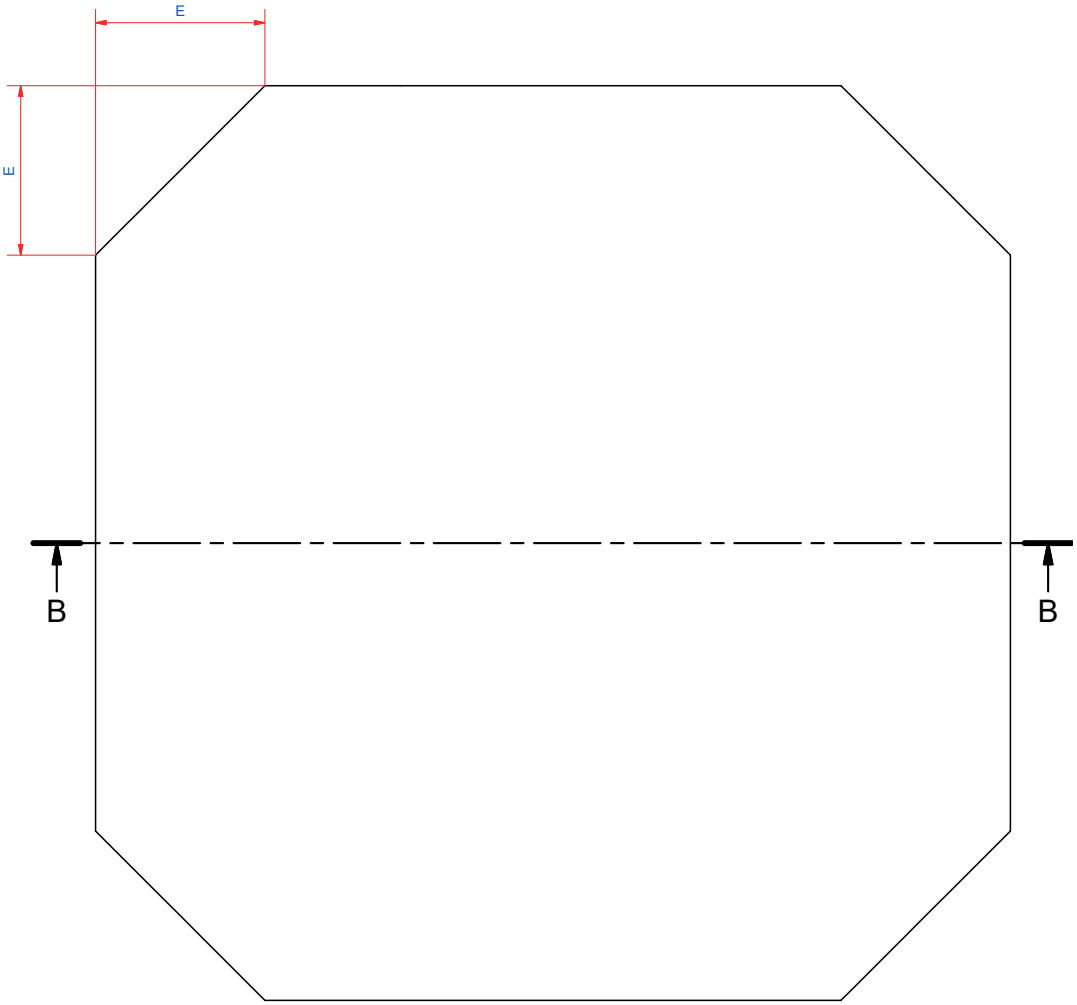


- Die Bodenplatte aus Stahlbeton ist von einem Fachunternehmen nach Klärung der Bodenverhältnisse herzustellen. Es ist auf die Ebenheitstoleranz nach DIN 18202 Zeile 4 erhöhte Anforderungen und eine ordentliche, zugeriebene und geglättete Oberfläche zu achten.
- Fundamente sollten bei Aufstellung mehrerer Silos in regelmäßigen Abständen Dehnungsfugen aufweisen.
- Das Gelände muss um das Silo herum angefüllt und geschottert sein.

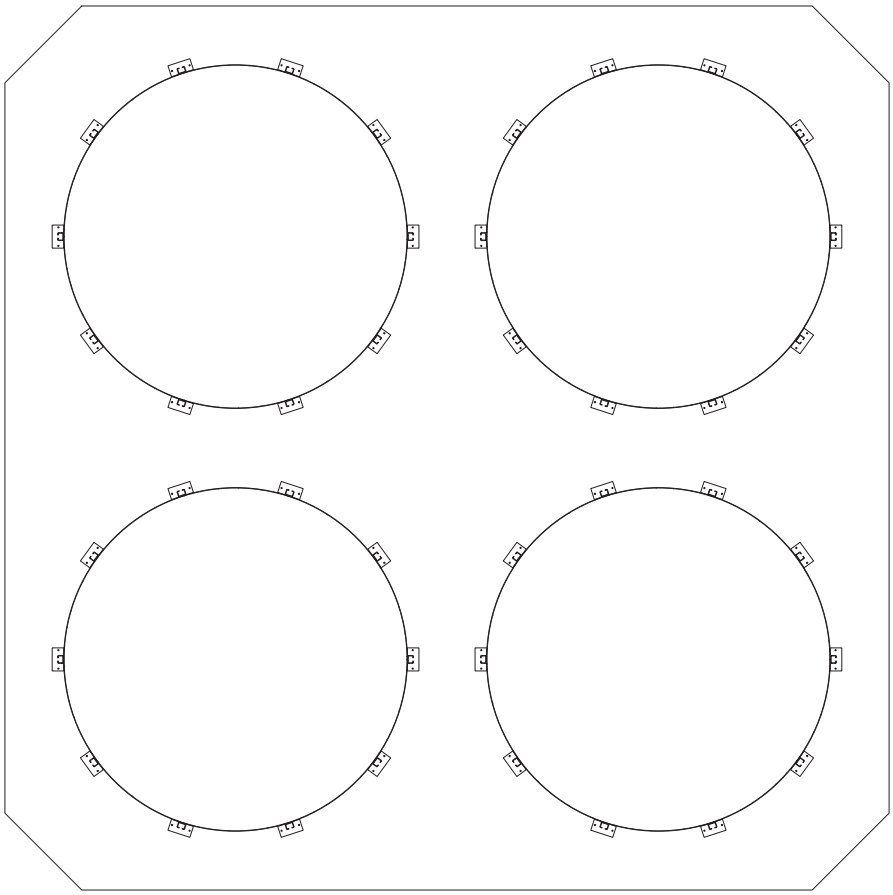

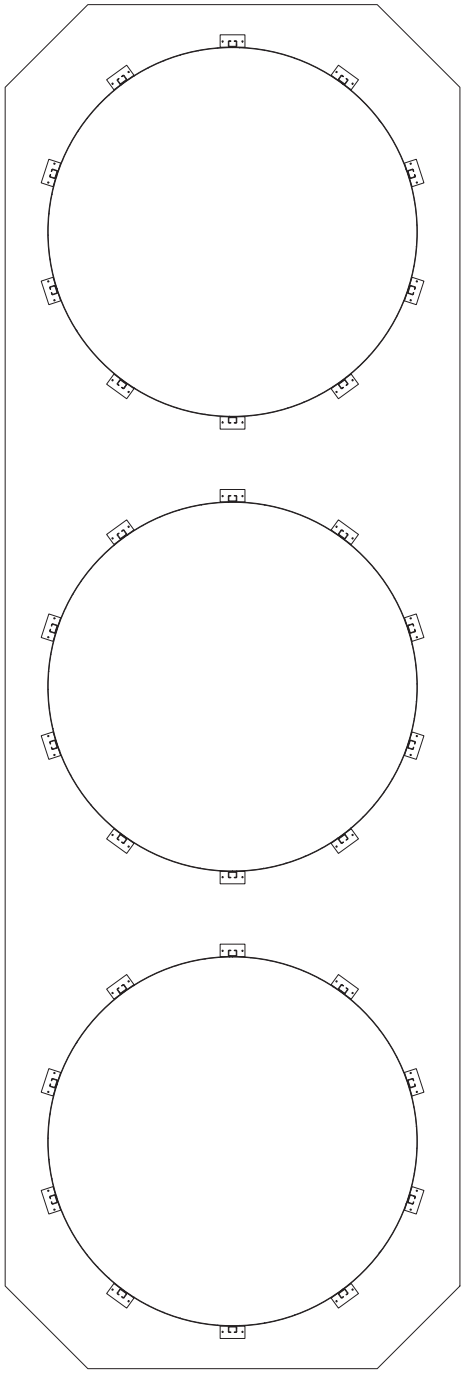


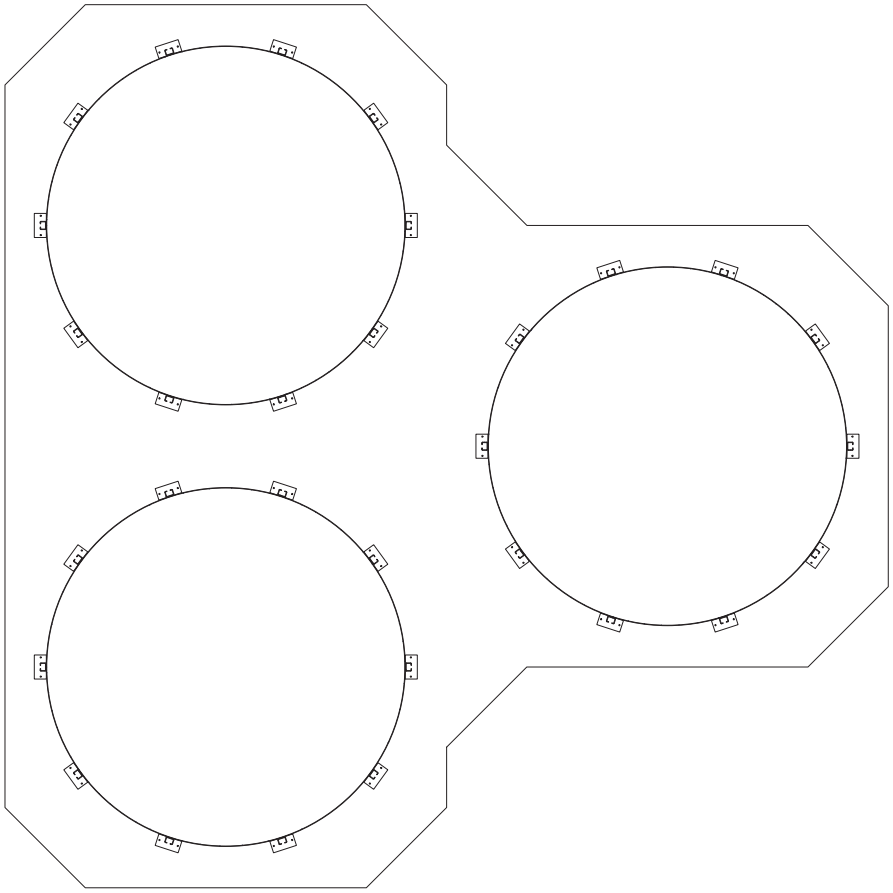


Belüftungseinrichtung NL3-NL8

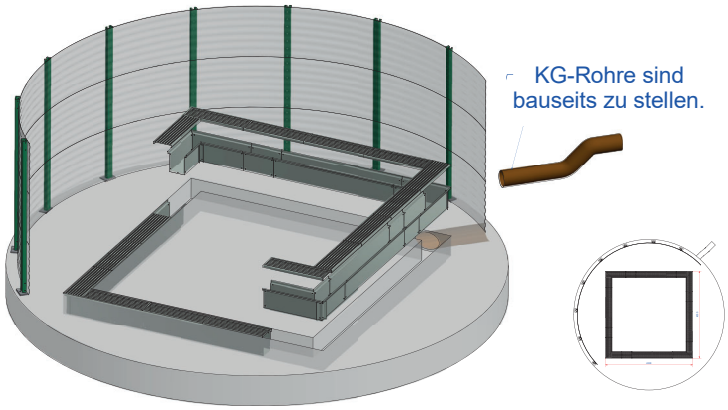

Belüftungseinrichtung NL9-NL16

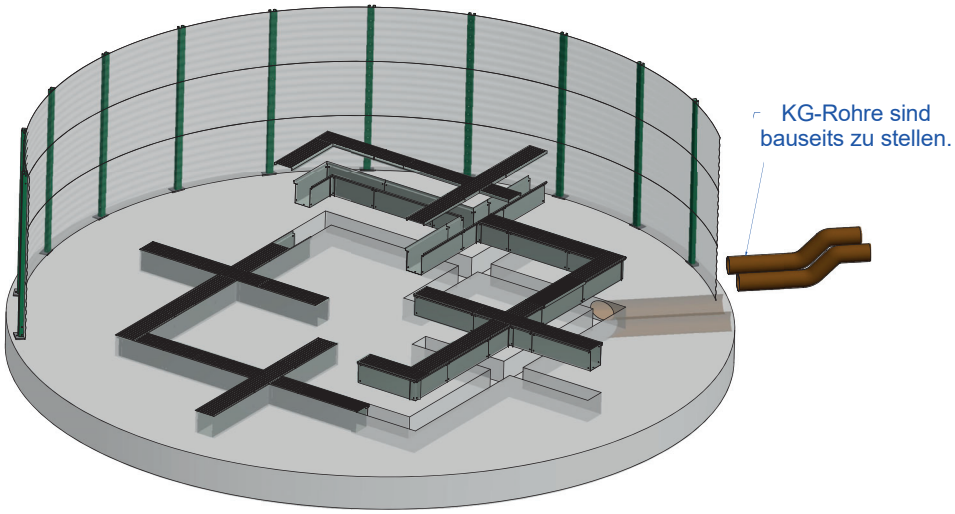


Belüftungseinrichtung NL20

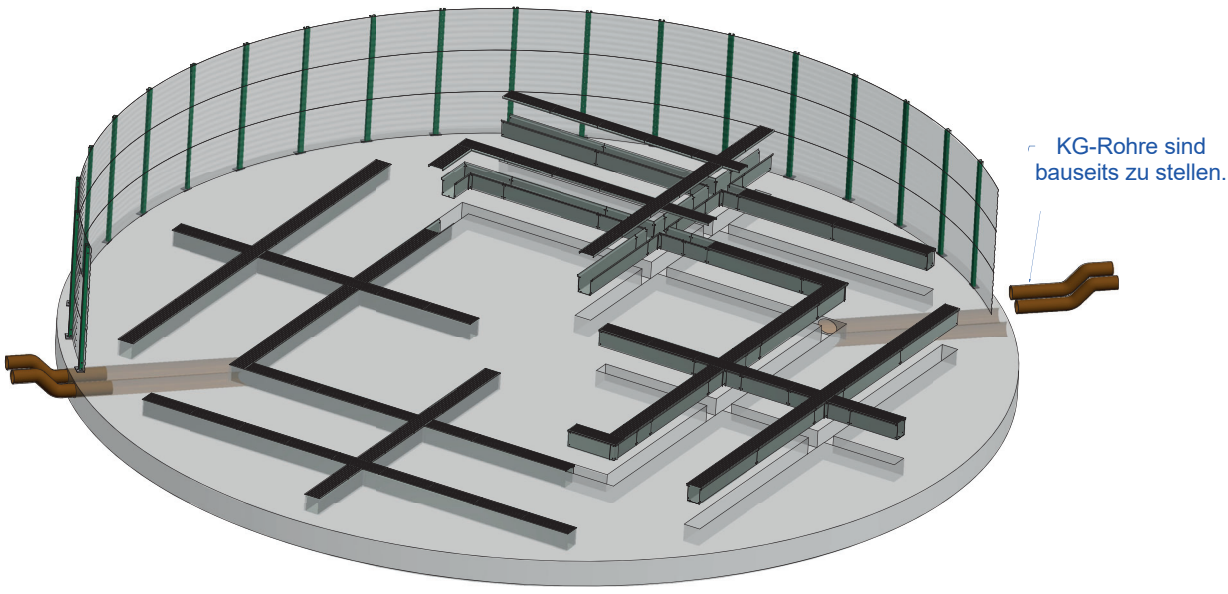


Belüftungseinrichtung NL3-NL8

NL 8 D=7,15 m

Anordnung verlorene Schalung (Blechkanal)

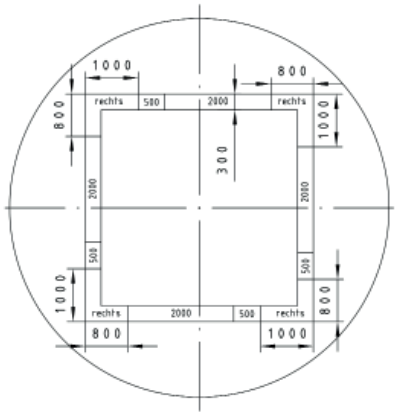


Kiemenplattenanordnung

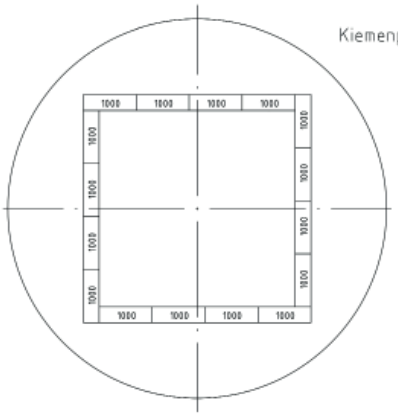

Belüftungseinrichtung NL9-NL16


NL 10 D=8,94 Verlorene Schalung

NL 11 D=9,83 Verlorene Schalung

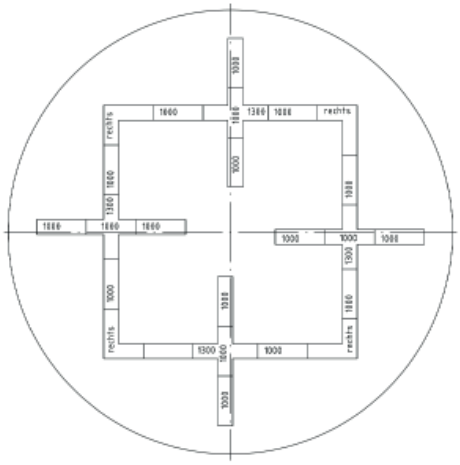


NL 10 D=8,94 Kiemenplatten

NL 11 D=9,83 Kiemenplatten

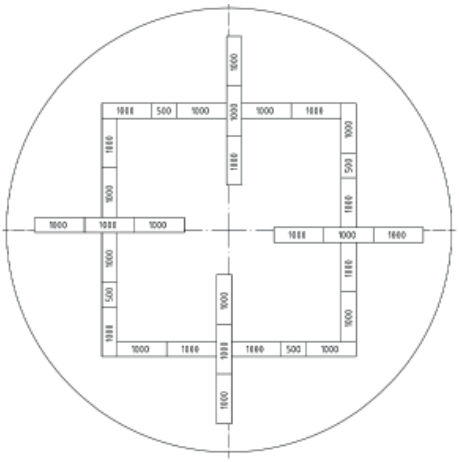


Belüftungseinrichtung NL20


NL20 D=17,88 m Verlorene Schalung

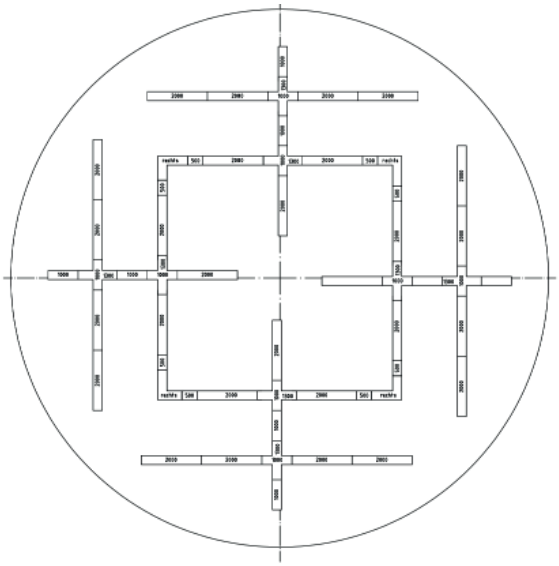

NL20 D=17,88 m Kiemenplatten

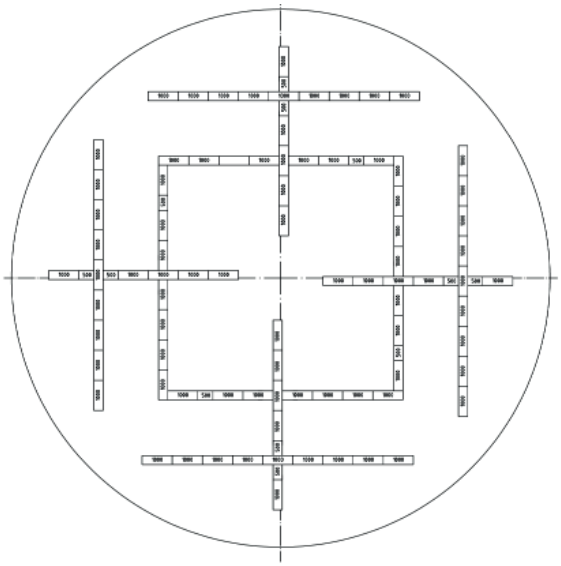

Lagersilo NLI mit Stützen - Innenaufstellung

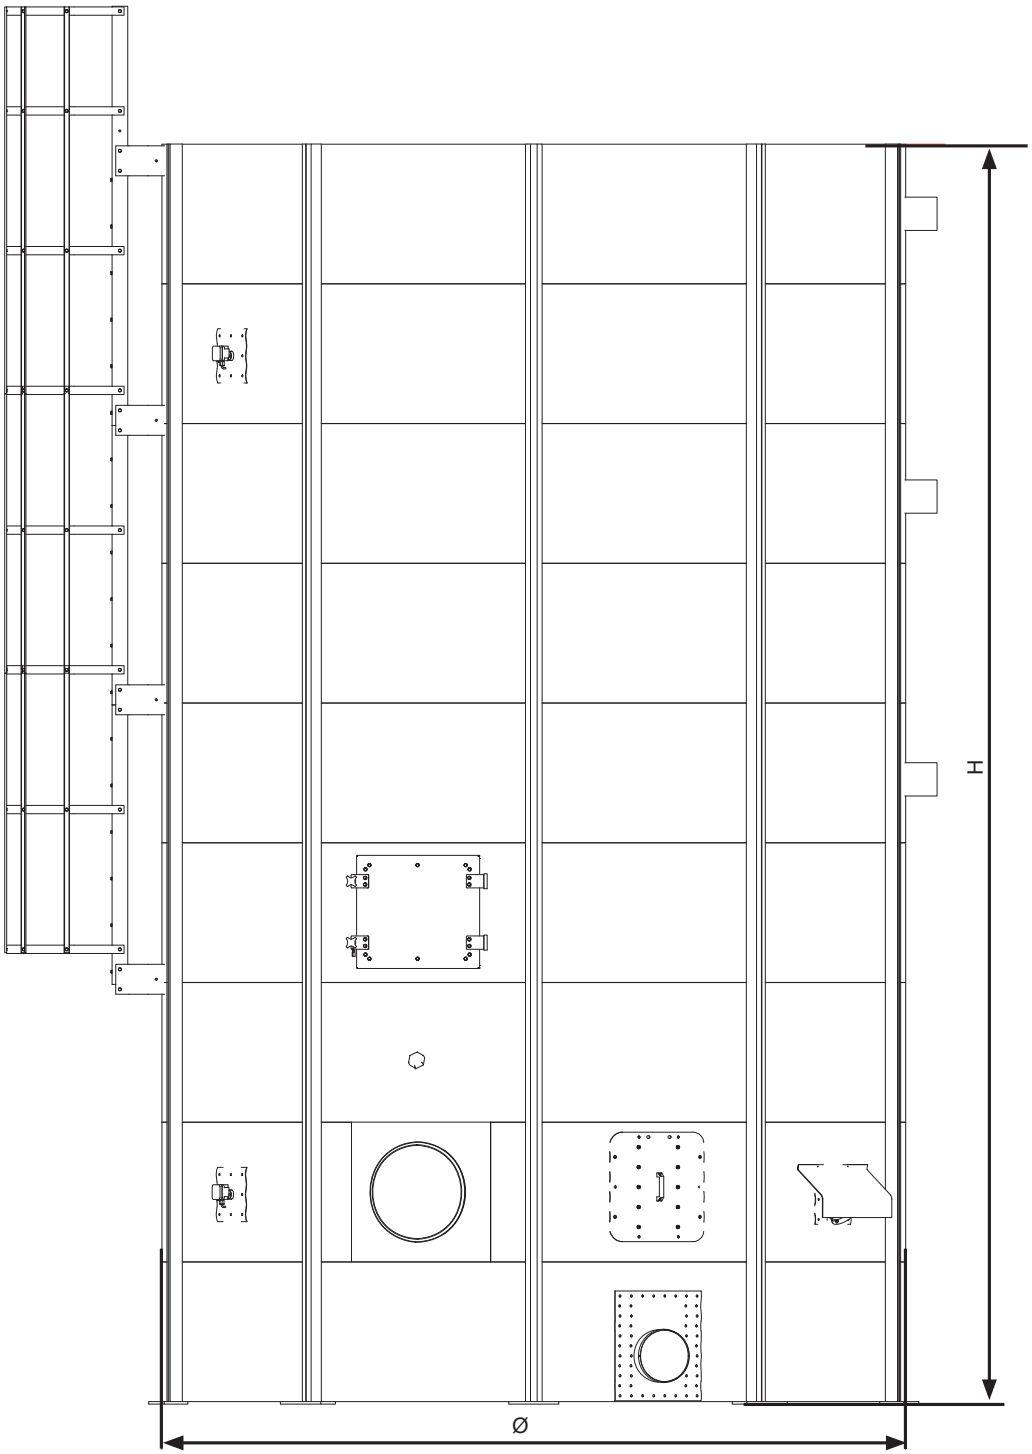


Lagersilo NLI mit Stützen - Innenaufstellung

Lagersilo NLI,mit Stützen, Innenaufstellung, verzinkte Siloplatten mit flacher Profilierung, verzinkte C-Stützen,feuerverzinkte Verschraubung,verzinkte Fußplatten, Schwerlastanker

Ringe [Anzahl]	Zylinderhöhe [m]	Typ Ø	NLI 2 1,79	NLI 2,5 2,23	NLI 3 2,68	NLI 3,5 3,13	NLI 4 3,58	NLI 4,5 4,02	NLI 5 4,47	NLI 5,5 4,92	NLI 6 5,36	NLI 7 6,26
3	**2,61**	Art.Nr.	4801602	4780030	4806602	4780230	4812602	4780430		4780640		
		[m³]	6,6	10,2	14,7	20,1	26,3	33,1		49,6		
		[t]	4,9	7,6	11,0	15,1	19,7	24,8		37,2		
4	**3,45**	Art.Nr.	4802102	4780040	4807102	4780240	4813102	4780440		4780650		
		[m³]	8,7	13,5	19,5	26,5	34,7	43,8		65,6		
		[t]	6,5	10,1	14,6	19,9	26,0	32,8		49,2		
5	**4,29**	Art.Nr.	4802602	4780050	4807602	4780250	4813602	4780450	4818102	4780660	4825602	4833602
		[m³]	10,8	16,8	24,2	33,0	43,2	54,5	67,3	81,6	96,8	132,0
		[t]	8,1	12,6	18,2	24,8	32,4	40,8	50,5	61,2	72,6	99,0
6	**5,13**	Art.Nr.	4803102	4780060	4808102	4780260	4814102	4780460	4818602	4780670	4826102	4834102
		[m³]	12,9	20,0	28,9	39,5	51,6	65,1	80,5	97,5	115,8	157,9
		[t]	9,7	15,0	21,7	29,6	38,7	48,8	60,4	73,1	86,8	118,4
7	**5,97**	Art.Nr.	4803602	4780070	4808602	4780270	4814602	4780470	4819102	4780680	4826602	4834602
		[m³]	15,0	23,3	33,7	45,9	60,1	75,8	93,7	113,5	134,7	183,7
		[t]	11,3	17,5	25,3	34,5	45,1	56,8	70,3	85,1	101,0	137,8
8	**6,81**	Art.Nr.	4804102	4780080	4809102	4780280	4815102	4780480	4819602	4780690	4827102	4835102
		[m³]	17,1	26,6	38,4	52,4	68,5	86,4	106,9	129,5	153,7	209,6
		[t]	12,9	19,9	28,8	39,3	51,4	64,8	80,2	97,1	115,2	157,2
9	**7,65**	Art.Nr.	4804302	4780090	4809602	4780290	4815602	4780490	4820102	4780691	4827602	4835602
		[m³]	19,3	29,9	43,2	58,9	77,0	97,1	120,1	145,4	172,6	235,5
		[t]	14,4	22,4	32,4	44,1	57,8	72,8	90,0	109,1	129,5	176,6
10	**8,49**	Art.Nr.	4804502	4780100	4810102	4780300	4816102	4780500	4820602			
		[m³]	21,4	33,2	47,9	65,3	85,5	107,8	133,2			
		[t]	16,0	24,9	35,9	49,0	64,1	80,8	99,9			
11	**9,33**	Art.Nr.								4780693		
		[m³]								177,4		
		[t]								133,0		
12	**10,17**	Art.Nr.								4780694		
		[m³]								193,3		
		[t]								145,0		

Zubehör	Typ	NLI 2	NLI 2,5	NLI 3	NLI 3,5	NLI 4	NLI 4,5	NLI 5	NLI 5,5	NLI 6	NLI 7
Belüftungseinrichtung											
Belüftungseinrichtung D150 für 3 - 10 Ringe (Halbrunde vollgelochte Kanäle mit Anschlusszubehör)	**Art.Nr.**	3882200					3882300		3883100		
Belüftungseinrichtung N/150 bis 10 Ringe (Belüftungsschläuche mit Anschlusszubehör)	**Art.Nr.**	3879102	3879112		3879122		3879132		3879142		
Abdeckung Silozylinder Kosa											
Abdeckung aus Polyesternadelfilz, weiß mit Einlaufstutzen, Halteschlaufen und Kordel	**Art.Nr.**	3210705	3210700	3210710	3210720	3210730	3210740	3210750	3210760	3210770	-
Einstiegstür											
Einstiegstür 560mm x 500mm mit Mantelplatte	**Art.Nr.**	3442610	3442620		3442630		3442640		3442650		3860060
Entnahmetechnik oberflur											
Entnahmerohr Ø 310mm bis 5 Ringe	**Art.Nr.**	3449000					3449400		-	-	-
Entnahmerohr Ø 310mm stabile Ausführung	**Art.Nr.**	3449100	3449200		3449300		3449500		3449600		
Rohrschutzkappe Ø 310, innen 313 mm	**Art.Nr.**	8210975									
Rohrschutzkappe Ø 310 außen 323,9 mm, mit Normaschelle S 326/20 zur Befestigung	**Art.Nr.**	8210965									
Rohrschutzkappe für Entnahmerohrmuffe, verschraubbar	**Art.Nr.**	4918000									
Messstutzen											
Messstutzen für Rundsilo NL mit Gewinde und Schutzkappe	**Art.Nr.**	7001025									
Messstutzen für Rundsilo NL mit Kunststoffabdeckkappe	**Art.Nr.**	4915500									
Siloabdichtung											
Abdichtungsmaterial Silowand/Beton bestehend aus: je 1 Dichtblech pro Siloplatte,1,5 Beutel Mastic pro Platte und Primer	**Art.Nr.**	-	3860030		3860040		3860050		3860060		

NL2 - NL11 Silos zur Außenaufstellung sind erhältlich mit Schneckenaustragung, mobiler Fegeschnecke oder stationärer Fegeschnecke

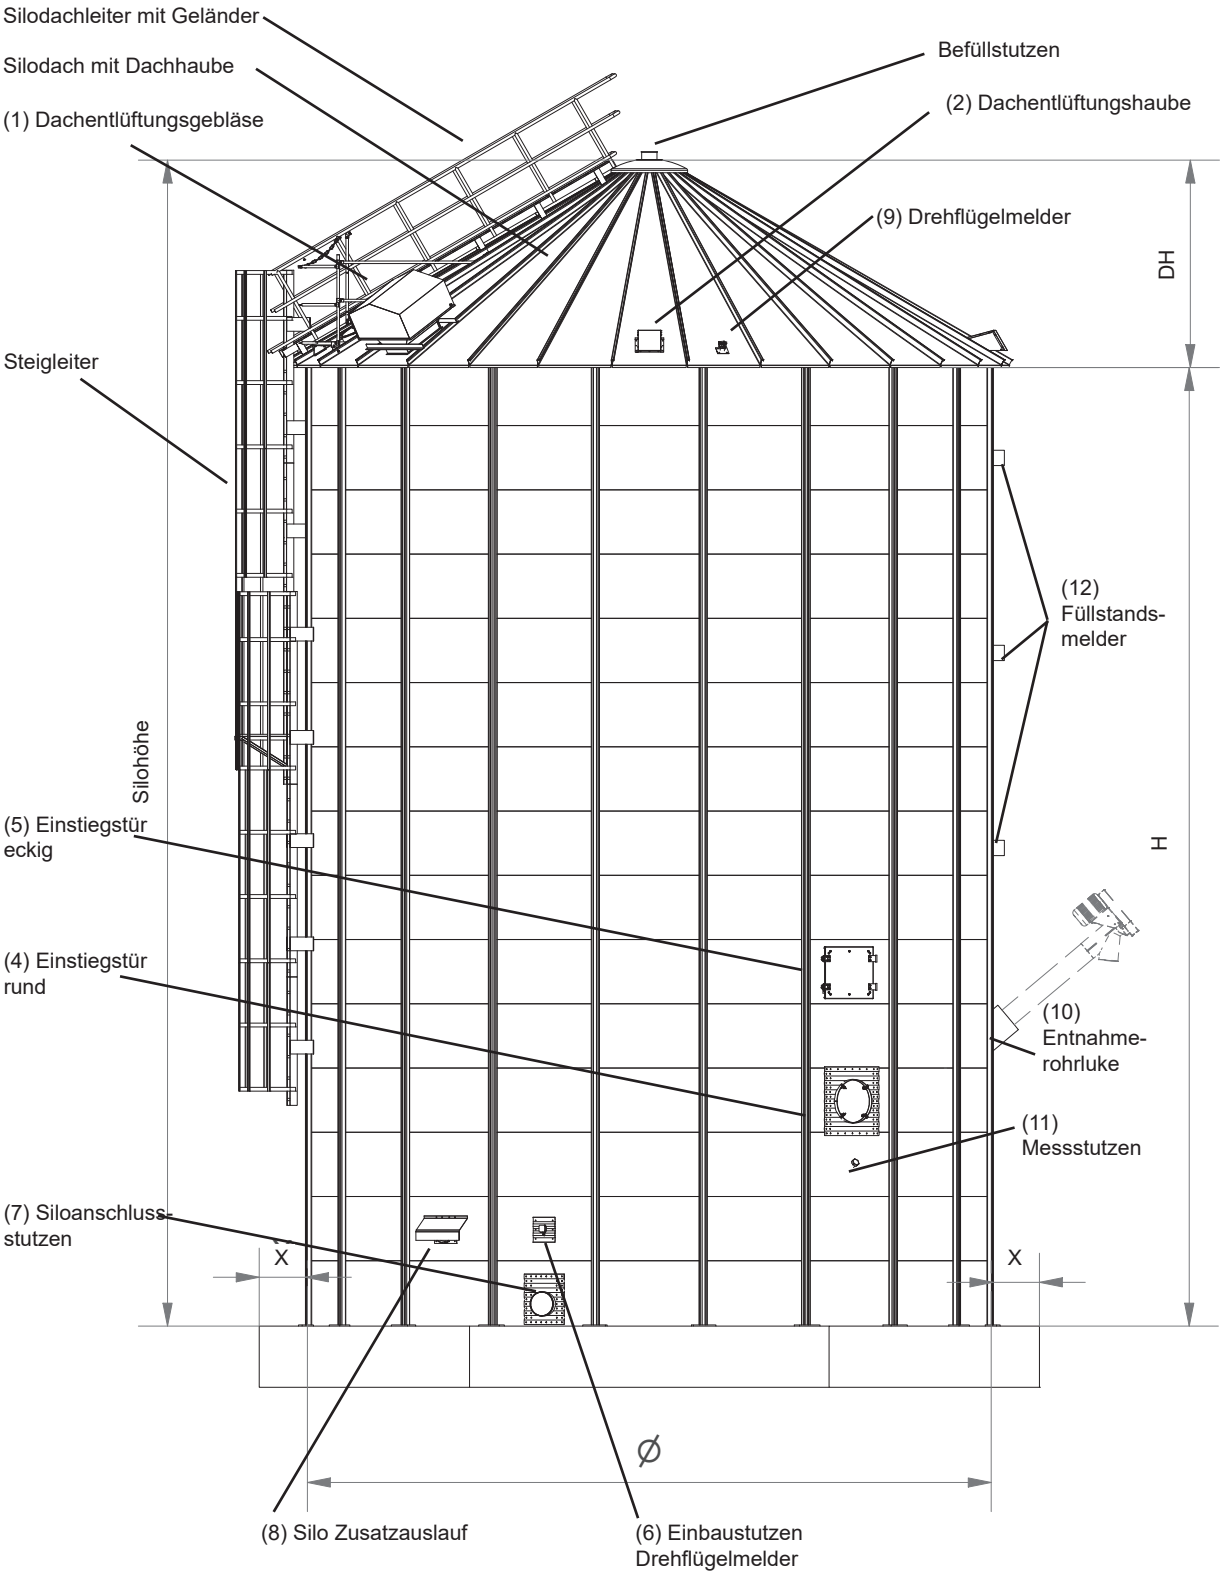

Lagersilo NL 2 - 11

Lagersilo NL, mit Stützen, Außenaufstellung, verzinkte Siloplatten mit flacher Profilierung, verzinkte C-Stützen, feuerverzinkte Verschraubung,rostfreie Verankerung, Dichtmaterial


Ringe [Anzahl]	Zylinderhöhe [m]	Typ Ø	NL 2 1,79	NL 3 2,68	NL 4 3,58	NL 5 4,47	NL 6 5,36	NL 7 6,26	NL 8 7,15	NL 9 8,04	NL 10 8,94	NL 11 9,83
5	**4,29**	Art.Nr.	4802601	4807601	4813601	4818101	4825601	4833601				
		[m³]	10,8	24,2	43,2	67,3	96,8	132,0				
		[t]	8,1	18,2	32,4	50,5	72,6	99,0				
6	**5,13**	Art.Nr.	4803101	4808101	4814101	4818601	4826101	4834101				
		[m³]	12,9	28,9	51,6	80,5	115,8	157,9				
		[t]	9,7	21,7	38,7	60,4	86,8	118,4				
7	**5,97**	Art.Nr.	4803601	4808601	4814601	4819101	4826601	4834601	4842601	4850601	4858601	4864330
		[m³]	15,0	33,7	60,1	93,7	134,7	183,7	239,7	303,1	374,7	453,1
		[t]	11,3	25,3	45,1	70,3	101,0	137,8	179,8	227,3	281,1	339,8
8	**6,81**	Art.Nr.	4804101	4809101	4815101	4819601	4827101	4835101	4843101	4851101	4859101	4864340
		[m³]	17,1	38,4	68,5	106,9	153,7	209,6	273,4	345,7	427,5	516,8
		[t]	12,9	28,8	51,4	80,2	115,2	157,2	205,1	259,3	320,6	387,6
9	**7,65**	Art.Nr.	4804301	4809601	4815601	4820101	4827601	4835601	4843601	4851601	4859601	4864350
		[m³]	19,3	43,2	77,0	120,1	172,6	235,5	307,2	388,4	480,2	580,6
		[t]	14,4	32,4	57,8	90,0	129,5	176,6	230,4	291,3	360,2	435,4
10	**8,49**	Art.Nr.	4804501	4810101	4816101	4820601	4828101	4836101	4844101	4852101	4860101	4863955
		[m³]	21,4	47,9	85,5	133,2	191,6	261,3	340,9	431,0	532,9	644,3
		[t]	16,0	35,9	64,1	99,9	143,7	196,0	255,7	323,3	399,7	483,2
11	**9,33**	Art.Nr.		4810201	4816201	4821101	4828601	4836601	4844601	4852601	4860601	4863960
		[m³]		52,6	93,9	146,4	210,5	287,2	374,6	473,7	585,7	708,1
		[t]		39,5	70,4	109,8	157,9	215,4	281,0	355,3	439,2	531,1
12	**10,17**	Art.Nr.		4810301	4816301	4821601	4829101	4837101	4845101	4853101	4861101	4863970
		[m³]		57,4	102,4	159,6	229,5	313,0	408,3	516,3	638,4	771,8
		[t]		43,0	76,8	119,7	172,1	234,8	306,3	387,2	478,8	578,9
13	**11,01**	Art.Nr.		4810401	4816401	4822101	4829601	4837601	4845601	4853601	4861601	4863980
		[m³]		62,1	110,8	172,8	248,4	338,9	442,1	559,0	691,1	835,6
		[t]		46,6	83,1	129,6	186,3	254,1	331,6	419,2	518,3	626,7
14	**11,85**	Art.Nr.		4810501	4816501	4822601	4830101	4838101	4846101	4854101	4862101	4864390
		[m³]		66,8	119,3	186,0	267,4	364,7	475,8	601,6	743,8	899,3
		[t]		50,1	89,5	139,5	200,5	273,5	356,8	451,2	557,9	674,5
15	**12,69**	Art.Nr.		4810601	4816601	4823101	4830601	4838601	4846601	4854601	4862601	4864400
		[m³]		71,6	127,7	199,1	286,3	390,6	509,5	644,3	796,6	963,1
		[t]		53,7	95,8	149,4	214,8	292,9	382,1	483,2	597,4	722,3
16	**13,53**	Art.Nr.			4816701	4823601	4831101	4839101	4847101	4855101	4863101	4864410
		[m³]			136,2	212,3	305,3	416,4	543,3	686,9	849,3	1026,8
		[t]			102,1	159,2	229,0	312,3	407,4	515,2	637,0	770,1
17	**14,37**	Art.Nr.			4816801	4823701	4831601	4839601	4847601	4855601	4863601	4864420
		[m³]			144,6	225,5	324,2	442,3	577,0	729,6	902,0	1090,6
		[t]			108,5	169,1	243,2	331,7	432,7	547,2	676,5	817,9
18	**15,21**	Art.Nr.			4816901	4823801	4832101	4839801	4847801	4855801	4863801	4864430
		[m³]			153,1	238,7	343,2	468,1	610,7	772,2	954,8	1154,3
		[t]			114,8	179,0	257,4	351,1	458,0	579,2	716,1	865,7
19	**16,05**	Art.Nr.			4817001	4823901	4832201	4839901	4847901	4855901	4863901	4864440
		[m³]			161,6	251,9	362,2	494,0	644,4	814,8	1007,5	1218,1
		[t]			121,2	188,9	271,6	370,5	483,3	611,1	755,6	913,6
20	**16,89**	Art.Nr.				4824001	4832301	4840001	4848001	4856001	4864001	4864450
		[m³]				265,1	381,1	519,8	678,2	857,5	1060,2	1281,8
		[t]				198,8	285,8	389,9	508,6	643,1	795,2	961,4
21	**17,73**	Art.Nr.				4824101	4832401	4840101	4848101	4856101	4864101	4864460
		[m³]				278,2	400,1	545,7	711,9	900,1	1112,9	1345,6
		[t]				208,7	300,0	409,3	533,9	675,1	834,7	1009,2
22	**18,57**	Art.Nr.				4824201	4832501	4840201	4848201	4856201	4864201	4864470
		[m³]				291,4	419,0	571,5	745,6	942,8	1165,7	1409,3
		[t]				218,6	314,3	428,7	559,2	707,1	874,3	1057,0
Silodach NL3- NL11 mit Dachhaube und Dachluke (NL2 ohne Dachluke)		Art.Nr.	4899980	4889900	4890000	4890100	4890200	4890300	4890400	4890500	4890610	4890710
		Höhe	0,5	0,72	1,08	1,36	1,59	1,85	2,11	2,37	2,56	2,82
		Vol	0,4	1,41	3,37	6,61	11,45	18,25	27,28	38,88	53,46	71,79

Die Inhaltsangaben basieren auf einem Schüttgewicht von 750 kg/m³ (nur zylindrische Höhe)

Zubehör NL 2 - 11

Zubehör	Typ	NL 2	NL 3	NL 4	NL 5	NL 6	NL 7	NL 8	NL 9	NL 10	NL 11
Dachverstärkung											
Dachverstärkung für den Einbau einer Temperaturmessanlage	Art.Nr.	-	-	4870000	4870100	4870200	4870250	4870300	4870450	4870500	4870600
Dachverstärkung für den Einbau einer Temperaturmeßanlage f. NL 9 ab 26 Ringe	Art.Nr.	-	-	-	-	-	-	-	4870460	-	-
Dachverstärkung für den Einbau einer Temperaturmeßanlage f. NL 10 ab 22 Ringe	Art.Nr.	-	-	-	-	-	-	-	-	4870510	-
Dachverstärkung für den Einbau einer Temperaturmessanlage f.NL 11 ab 19 Ringe	Art.Nr.	-	-	-	-	-	-	-	-	-	4870610
Dachleitern											
Dachleiter mit Geländer für NL	Art.Nr.	-	4899100	4899110	4899120	4899130	4899140	4899150	4899160	4899170	4899180
Befüllstutzen											
Befüllstutzen Ø 150 = GUMA DS Verbindung	Art.Nr.	4958400									
Befüllstutzen Ø 150 = Spannring Verbindung	Art.Nr.	4958450									
Befüllstutzen Ø 150 = FS- Verbindung	Art.Nr.	4958500									
Dichtung für FS - Verbindung	Art.Nr.	0040227									
Befüllstutzen Ø 200 = Spannring Verbindung	Art.Nr.	4958550									
Befüllstutzen Ø 250 = Spannring Verbindung	Art.Nr.	4958700									
Dachhaube ND für NL 3-11 Einlauf Ø 300 mm, mit Befüllstutzen	Art.Nr.	4881115									
Dachentlüftung											
Entlüftungshaube 300x300mm für Silodach NL	Art.Nr.	4958330									
Dachentlüftungsgebläse NDE für NL-Silos mit Neigung 30° bzw. 25° bestehend aus: verzinkter Abdeckhaube, Lüfter mit Motor 0,55 kW EX - ATEX 21, Luftleistung freiblasend 7.400 m³/h	Art.Nr.	5302800									
Entnahmetechnik oberflur (Entnahmerohr)											
Entnahmerohre Gr. 310 mit Luke	Art.Nr.	3448002	3448102	3448202	3448302	3448402	3448502	3448602	3448702	3448802	-
Kappe Entnahmerohrmuffe Ø 310, außen 323,9 mm, verschraubbar, mit Montagepaket	Art.Nr.	4918000									
Entnahmerohrluke Gr. 400	Art.Nr.	3451005	3451000		3451010		3451020			3451030	
Für eine komplette Siloentnahme werden Entnahmerohrluke, Entnahmerohr und Abdeckhaube benötigt.											
Entnahmerohr Ø 400, 6 m lang, lackiert, 6,3 mm stark **(Länge ist bauseits anzupassen)**	Art.Nr.	4922000									
Entnahmerohrunterbauten für NL für Ø 310 und Ø 400	Art.Nr.	-	-	-	4923204		4923206			4923209	
Abdeckhaube S200, für Entnahmerohrluke Ø 400	Art.Nr.	8140900									
Abdeckhaube S250, für Entnahmerohrluke Ø 400	Art.Nr.	8140700									
Abdeckhaube S300, für Entnahmerohrluke Ø 400	Art.Nr.	7013643									
Rohrschutzkappe für Entnahmerohrmuffe Ø 400 (Rohrschutzkappe flexibel Ø 419 x 90)	Art.Nr.	8210980									
Abdeckhaube S300, für Entnahmerohrluke Ø 500	Art.Nr.	7002993									
Entnahmerohr Ø 500, 6 m lang, lackiert, 6,3 mm stark **(Länge ist bauseits anzupassen)**	Art.Nr.	-	-	-	-	-	4922100	-	-	-	-
Messstutzen und Vollmelder											
Messstutzen NL mit Schutzkappe und Torro-Schelle	Art.Nr.	4915500									
Messstutzen für Rundsilo NL mit Gewinde und Schraubkappe	Art.Nr.	7001025									
Drehflügelmelder mit Kunststoffflügel und 75 mm Welle, 230 V AC	Art.Nr.	3459000									
Drehflügelmelder mit Kunststoffflügel und 75 mm Welle, 24 V DC	Art.Nr.	3459150									
Bausatz für Pendelwelle L=500 mm	Art.Nr.	3459160									
Bausatz für Pendelwelle L=1000 mm	Art.Nr.	3459170									
Bausatz Seilverlängerung 2 m	Art.Nr.	3459180									
Einbaustutzen Drehflügelmelder am Silozylinder	Art.Nr.	3459800									
Einbaustutzen Drehflügelmelder am Silodach (30°)	Art.Nr.	3459500									
Einstiegluken											
Einstiegluke Ø 560 rund	Art.Nr.	3450490	3450530			3450540			3450550		3450560
Einstiegluke eckig 700 x 600 mm, mit Einsetzlamellen	Art.Nr.	3446000				3446010			3446020		
Einstiegluke eckig für doppelte Stützenreihe	Art.Nr.	-	3445606			3445605			3445705		
Notauslauf Ø200 45° NL-Silo - verzinkt - **Nur zur kontrollierten Restentleerung!**	Art.Nr.	3457800									
Einstiegsgriff für Einstiegsluke	Art.Nr.	4881160									
Einstieghilfe zweistufig für NL-Silo, vormontiert	Art.Nr.	3420080									
Einstiegstufe dreistufig, für NL-Silo	Art.Nr.	3420085									
Wartungsbühne für NL-Silo, komplett	Art.Nr.	3420260									
Unterflurbelüftung											
Unterflurbelüftung bestehend aus Verschalungen, Kiemenplatten light B=300mm, Winkel, T-Stück und Enddeckel. **KG-Rohre zur Luftzufuhr sind bauseitig beizustellen.**	Art.Nr.	-	3884000		3884100	3884200	3884300	3884400	3884500	3884600	
Siloanschlussstutzen Ø 310, NL	Art.Nr.	8210980									
Rohrschutzkappe Ø 310, innen 313 mm, für Rohr Ø 310, Rohrschellenverbindung	Art.Nr.	-	-	3099900	3099910	3099920	3099930	3100200	3100300	-	-
Auslaufschieber											
Schieber 200x200 elektrisch	Art.Nr.	4495100									
Schieber 250x250 elektrisch	Art.Nr.	4495000									
Schieber 250x250 fernbetätigt	Art.Nr.	4495010									
Schieber 250x250 handbetätigt	Art.Nr.	4495020									
Schieber 250x250 pneumatisch	Art.Nr.	1768540									
Schieber 300x300 elektrisch	Art.Nr.	4495040									
Schieber 300x300 fernbetätigt	Art.Nr.	4495050									
Schieber 300x300 handb Endschalt	Art.Nr.	4495080									
Schieber 300x300 handbetätigt	Art.Nr.	4495060									
Schieber 300x300 pneumatisch	Art.Nr.	4495070									

NL12 - NL 20 Silos zur Außenaufstellung sind erhältlich mit der stationären Fegeschnecke von NEUERO.

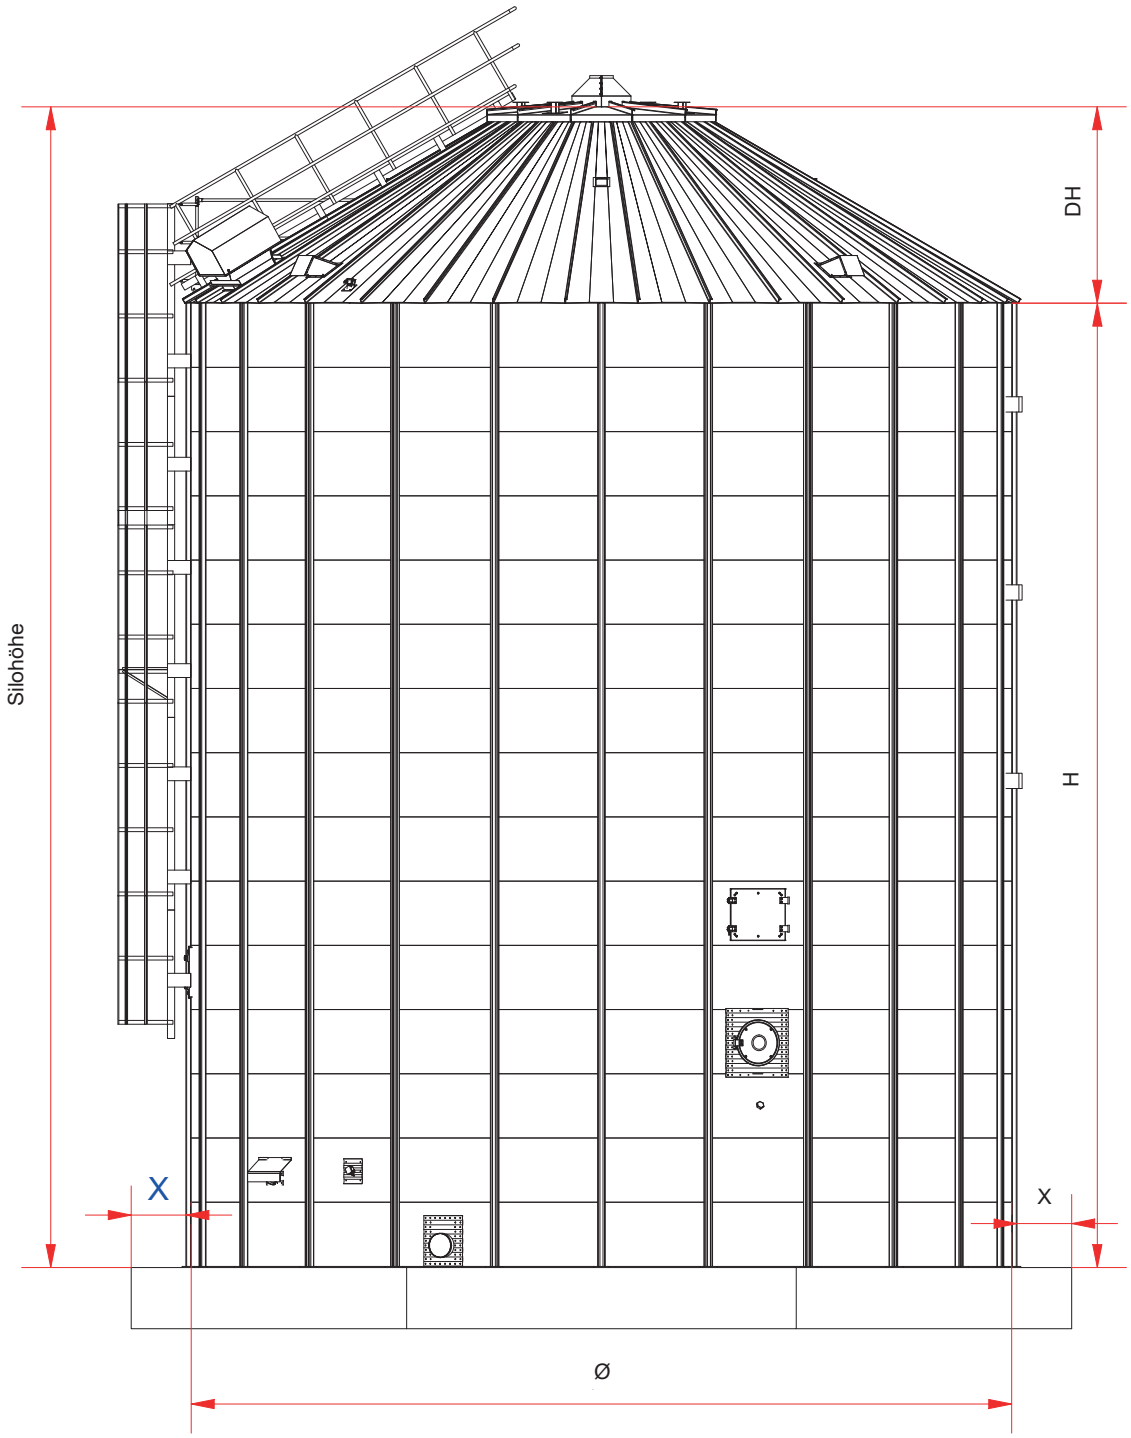


Lagersilo NL 12 - 20

Lagersilo NL, mit Stützen, Außenaufstellung, verzinkte Siloplatten mit flacher Profilierung, verzinkte C-Stützen, feuerverzinkte Verschraubung,rostfreie Verankerung, Dichtmaterial


Ringe [Anzahl]	Zylinderhöhe [m]	Typ Ø	NL 12 10,73	NL 13 11,62	NL 14 12,51	NL 16 14,3	NL 18 16,09	NL 20 17,88
7	**5,97**	Art.Nr.	4864930	4865110	4865380	4865530		
		[m³]	539,8	633,1	733,8	958,8		
		[t]	404,9	474,8	550,4	719,1		
8	**6,81**	Art.Nr.	4864940	4865120	4865390	4865540	4865701	4865850
		[m³]	615,8	722,2	837,1	1093,7	1384,7	1709,9
		[t]	461,8	541,6	627,8	820,3	1038,5	1282,4
9	**7,65**	Art.Nr.	4864950	4865130	4865400	4865550	4865702	4865860
		[m³]	691,8	811,3	940,3	1228,6	1555,5	1920,8
		[t]	518,8	608,4	705,2	921,5	1166,6	1440,6
10	**8,49**	Art.Nr.	4864960	4865140	4865401	4865560	4865703	4865870
		[m³]	767,7	900,3	1043,5	1363,5	1726,3	2131,7
		[t]	575,8	675,3	782,7	1022,7	1294,7	1598,8
11	**9,33**	Art.Nr.	4864970	4865150	4865402	4865565	4865704	4865880
		[m³]	843,7	989,4	1146,8	1498,5	1897,1	2342,6
		[t]	632,8	742,1	860,1	1123,8	1422,8	1757,0
12	**10,17**	Art.Nr.	4864980	4865160	4865403	4865570	4865700	4865900
		[m³]	919,6	1078,5	1250,0	1633,4	2067,9	2553,6
		[t]	689,7	808,9	937,5	1225,0	1550,9	1915,2
13	**11,01**	Art.Nr.	4864990	4865170	4865406	4865580	4865710	4865910
		[m³]	995,6	1167,6	1353,3	1768,3	2238,7	2764,5
		[t]	746,7	875,7	1015,0	1326,2	1679,0	2073,4
14	**11,85**	Art.Nr.	4864995	4865180	4865404	4865590	4865720	4865920
		[m³]	1071,5	1256,7	1456,5	1903,2	2409,5	2975,4
		[t]	803,7	942,5	1092,4	1427,4	1807,1	2231,5
15	**12,69**	Art.Nr.	4865000	4865190	4865405	4865600	4865730	4865930
		[m³]	1147,5	1345,7	1559,8	2038,1	2580,3	3186,3
		[t]	860,6	1009,3	1169,8	1528,6	1935,2	2389,7
16	**13,53**	Art.Nr.	4865010	4865200	4865410	4865610	4865740	4865940
		[m³]	1223,5	1434,8	1663,0	2173,0	2751,1	3397,2
		[t]	917,6	1076,1	1247,3	1629,8	2063,3	2547,9
17	**14,37**	Art.Nr.	4865020	4865210	4865420	4865620	4865750	4865950
		[m³]	1299,4	1523,9	1766,3	2307,9	2921,9	3608,1
		[t]	974,6	1142,9	1324,7	1730,9	2191,4	2706,1
18	**15,21**	Art.Nr.	4865030	4865220	4865430	4865630	4865760	4865960
		[m³]	1375,4	1613,0	1869,5	2442,8	3092,7	3819,0
		[t]	1031,5	1209,7	1402,2	1832,1	2319,5	2864,3
19	**16,05**	Art.Nr.	4865040	4865230	4865440	4865640	4865770	4865970
		[m³]	1451,3	1702,1	1972,8	2577,7	3263,5	4030,0
		[t]	1088,5	1276,6	1479,6	1933,3	2447,6	3022,5
20	**16,89**	Art.Nr.	4865050	4865240	4865450	4865650	4865780	4865980
		[m³]	1527,3	1791,1	2076,0	2712,6	3434,2	4240,9
		[t]	1145,5	1343,4	1557,0	2034,5	2575,7	3180,6
21	**17,73**	Art.Nr.	4865060	4865250	4865460	4865660	4865790	4865990
		[m³]	1603,2	1880,2	2179,3	2847,5	3605,0	4451,8
		[t]	1202,4	1410,2	1634,5	2135,7	2703,8	3338,8
22	**18,57**	Art.Nr.	4865070	4865260	4865470	4865670	4865800	4866000
		[m³]	1679,2	1969,3	2282,5	2982,5	3775,8	4662,7
		[t]	1259,4	1477,0	1711,9	2236,8	2831,9	3497,0
Silodach mit Dachhaube, mit Dachluke		Art.Nr.	**auf Anfrage**	**auf Anfrage**	**auf Anfrage**	**auf Anfrage**	**auf Anfrage**	**auf Anfrage**
		Höhe	2,92	3,03	3,17	3,63	4,2	4,6
		Vol	92,01	117,31	145,95	218,86	312,49	429,41

Lagersilo NL 12 - 20


Zubehör	Typ	NL 12	NL 13	NL 14	NL 16	NL 18	NL 20
Dachleiter							
Dachleiter mit Geländer für NL	Art.Nr. €	4899190 1360,-					
Dachentlüftung							
Entlüftungshaube 300x300 mm für Silodach NL	Art.Nr.	4958330					
„Dachentlüftungsgebläse NDE für NL-Silos mit Neigung 30° bzw. 25° bestehend aus: verzinkter Abdeckhaube, Lüfter mit Motor 0,55 kW EX - ATEX 21, Luftleistung freiblasend 7.400 m³/h“	Art.Nr. €	5302800					
Entnahmetechnik oberflur (Entnahmerohr)							
Entnahmerohrluke Gr. 400 Für eine komplette Siloentnahme werden Entnahmerohrluke, Entnahmerohr und Abdeckhaube benötigt.	Art.Nr.	3451030		3451025		3451100	
Entnahmerohr Ø 400, 6 m lang, lackiert, 6,3 mm stark, (Länge ist bauseits anzupassen	Art.Nr.	4922000					
Abdeckhaube S200 für Entnahmerohrluke Ø 400	Art.Nr.	8140900					
Abdeckhaube S250 für Entnahmerohrluke Ø 400	Art.Nr.	8140700					
Abdeckhaube S300 für Entnahmerohrluke Ø 400	Art.Nr.	8140811					
Einstiegluken							
Einstiegluke Ø 560 rund für doppelte Stützenreihe	Art.Nr.	3446130				3446140	
Notauslauf Ø200 45° NL-Silo - verzinkt - Nur zur kontrollierten Restentleerung!	Art.Nr.	4870600					
Einstiegsgriff für Einstiegsluke	Art.Nr.	4881160					
Einstieghilfe zweistufig für NL-Silo mit Handgriff (lose), vormontiert	Art.Nr.	3420080					
Einstiegstufe dreistufig, für NL-Silo ohne Handgriff	Art.Nr.	3420085					
Wartungsbühne für NL-Silo, komplett	Art.Nr.	3420260					
Unterflurbelüftung							
Unterflurbelüftung bestehend aus Verschalungen, Kiemenplatten light B=300mm, Winkel, T-Stück und Enddeckel. **KG-Rohre zur Luftzufuhr sind bauseitig beizustellen.**	Art.Nr.	3884700	3884710	3884800	3884900	3885000	3885200
Siloanschlussstutzen Ø 310, NL	Art.Nr.	8210980					
Auslaufschieber							
Schieber 200x200 elektrisch	Art.Nr.	4495100					
Schieber 250x250 elektrisch	Art.Nr.	4495000					
Schieber 250x250 fernbetätigt	Art.Nr.	4495010					
Schieber 250x250 handbetätigt	Art.Nr.	4495020					
Schieber 250x250 pneumatisch	Art.Nr.	1768540					
Schieber 300x300 elektrisch	Art.Nr.	4495040					
Schieber 300x300 fernbetätigt	Art.Nr.	4495050					
Schieber 300x300 handbetätigt Endschalt	Art.Nr.	4495080					
Schieber 300x300 handbetätigt	Art.Nr.	4495060					
Schieber 300x300 pneumatisch	Art.Nr.	4495070					

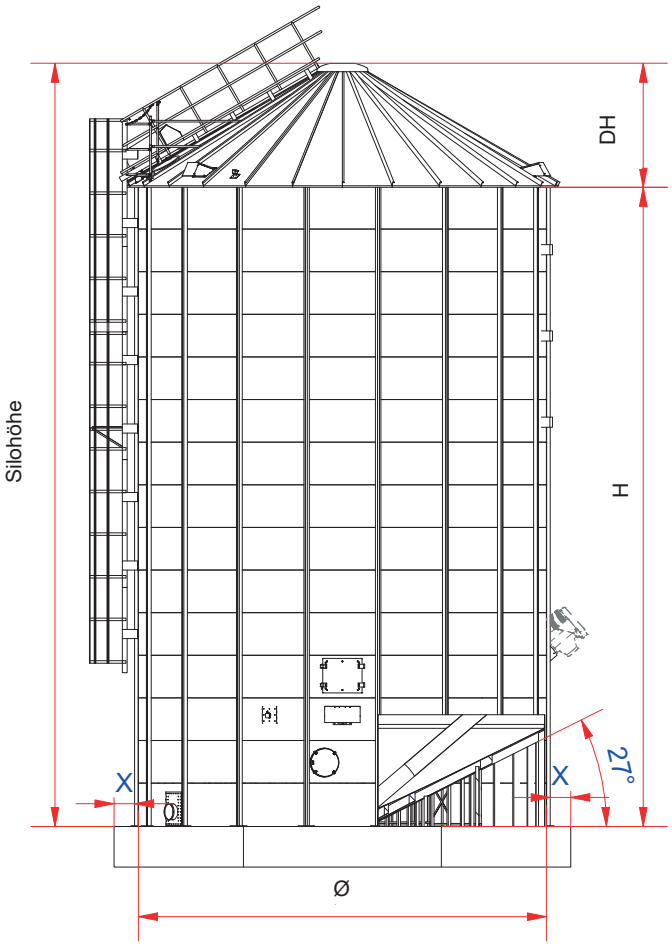


normaler Unterbau 27°

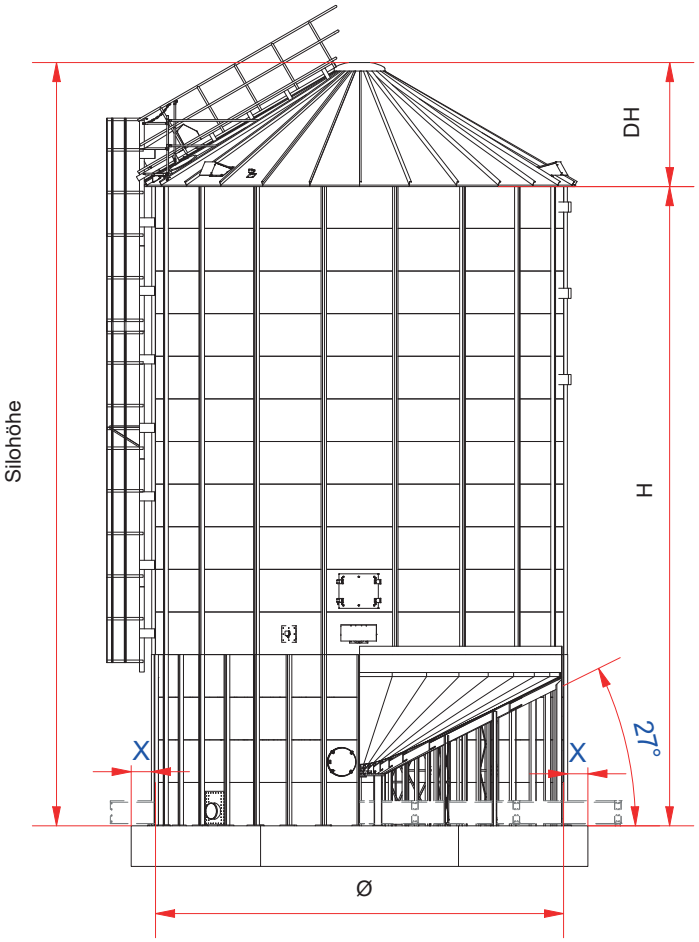

erhöhter Unterbau 27°

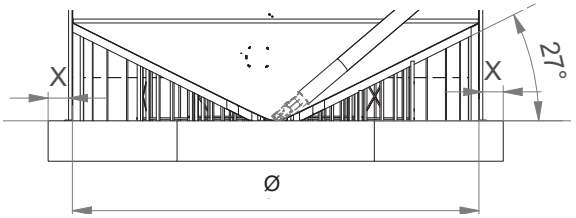


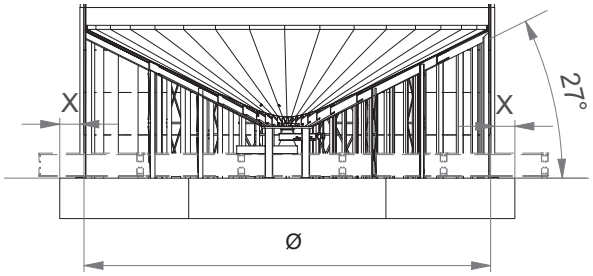


Lagersilo NLK 27° - Konus

Lagersilo NLK mit Stützen, für Belüftungskonus 27° normal + erhöht Innen-/Außenaufstellung, verzinkte Siloplatten mit flacher Profilierung, verzinkte C-Stützen, feuerverzinkte Verschraubung


Ringe	Zylinderhöhe Unterbau	Typ	NLK 4 normal	NLK 5 normal	NLK 6 normal	NLK 7 normal	NLK 8 normal	NLK 9 normal	NLK 4 erhöht	NLK 5 erhöht	NLK 6 erhöht	NLK 7 erhöht	NLK 8 erhöht	NLK 9 erhöht
[Anzahl]	[m]	Ø	3,58	4,47	5,36	6,26	7,15	8,04	3,58	4,47	5,36	6,26	7,15	8,04
5	**4,29**	Art.Nr.	4867000	4867100	4867200	4867300			4867000	4867100	4867200	4867300		
		[m³]	38,2	56,3	77,8	101			31,2	46,3	63,8	82		
		[t]	28,6	42,2	58,6	76			23,4	34,7	47,6	61		
6	**5,13**	Art.Nr.	4867001	4867101	4867201	4867301			4867001	4867101	4867201	4867301		
		[m³]	46,6	69,5	96,8	126,9			39,6	59,5	82,8	107,9		
		[t]	35,0	52,1	72,8	95,4			29,7	44,6	61,8	80,4		
7	**5,97**	Art.Nr.	4867002	4867102	4867202	4867302			4867002	4867102	4867202	4867302		
		[m³]	55,1	82,7	115,7	152,7			48,1	72,7	101,7	133,7		
		[t]	41,3	62,0	87	114,8			36,1	54,5	76	99,8		
8	**6,81**	Art.Nr.	4867003	4867103	4867203	4867303			4867003	4867103	4867203	4867303		
		[m³]	63,5	95,9	134,7	178,6			56,5	85,9	120,7	159,6		
		[t]	47,7	71,9	101,2	134,2			42,4	64,4	90,2	119,2		
9	**7,65**	Art.Nr.	4867004	4867104	4867204	4867304		4868013	4867004	4867104	4867204	4867304		4868013
		[m³]	72,0	109,1	153,6	204,5		322,4	65,0	99,1	139,6	185,5		290,4
		[t]	54,0	81,8	115,2	153,3		241,8	48,8	74,3	104,7	139,1		217,8
10	**8,49**	Art.Nr.	4867005	4867105	4867205	4867305			4867005	4867105	4867205	4867305		
		[m³]	80,5	122,2	172,6	230,3			73,5	112,2	158,6	211,3		
		[t]	60,3	91,7	129,4	172,7			55,1	84,2	118,9	158,5		
11	**9,33**	Art.Nr.	4867006	4867106	4867206	4867306		4868011	4867006	4867106	4867206	4867306		4868011
		[m³]	88,9	135,4	191,5	256,2		407,7	81,9	125,4	177,5	237,2		375,7
		[t]	66,7	101,6	143,6	192,1		305,8	61,4	94,1	133,1	177,9		281,8
12	**10,17**	Art.Nr.	4867007	4867107	4867207	4867307	4845710	4853102	4867007	4867107	4867207	4867307	4845710	4853102
		[m³]	97,4	148,6	210,5	282,0	363,3	450,3	90,4	138,6	196,5	263,0	336,3	418,3
		[t]	73,0	111,4	157,9	211,5	272,5	337,7	67,8	103,9	147,4	197,3	252,3	313,7
13	**11,01**	Art.Nr.	4867008	4867108	4867208	4867308	4845700	4868010	4867008	4867108	4867208	4867308	4845700	4868010
		[m³]	105,8	161,8	229,4	307,9	397,1	493,0	98,8	151,8	215,4	288,9	370,1	461,0
		[t]	79,4	121,3	172,1	230,9	297,8	369,7	74,1	113,8	161,6	216,6	277,6	345,7
14	**11,85**	Art.Nr.	4867009	4867109	4867209	4867309	4846103	4854102	4867009	4867109	4867209	4867309	4846103	4854102
		[m³]	114,3	175,0	248,4	333,7	430,8	535,6	107,3	165,0	234,4	314,7	403,8	503,6
		[t]	85,7	131,2	186,3	250,3	323,1	401,7	80,5	123,7	175,8	236,0	302,8	377,7
15	**12,69**	Art.Nr.	4867010	4867110	4867210	4867310	4846603	4868015	4867010	4867110	4867210	4867310	4846603	4868015
		[m³]	122,7	188,1	267,3	359,6	464,5	578,3	115,7	178,1	253,3	340,6	437,5	546,3
		[t]	92,1	141,1	200,5	269,7	348,4	433,7	86,8	133,6	190,0	255,4	328,1	409,7
16	**13,53**	Art.Nr.			4867670	4837311	4847401	4868019			4867670	4837311	4847401	4868019
		[m³]			286,3	385,4	498,3	620,9			272,3	366,4	471,3	588,9
		[t]			214,7	289,1	373,7	465,7			204,2	274,8	353,4	441,7
17	**14,37**	Art.Nr.				4867318	4867601	4868017				4867318	4867601	4868017
		[m³]				411,3	532,0	663,6				392,3	505,0	631,6
		[t]				308,5	399,0	497,7				294,2	378,7	473,7
18	**15,21**	Art.Nr.						4868018						4868018
		[m³]						706,2						674,2
		[t]						529,7						505,7
19	**16,05**	Art.Nr.						4856003						
		[m³]						748,8						
		[t]						561,6						
20	**16,89**	Art.Nr.					4847403	4856002					4847403	
		[m³]					633,2	791,5					606,2	
		[t]					474,9	593,6					454,6	
21	**17,73**	Art.Nr.					4847404						4847404	
		[m³]					666,9						639,9	
		[t]					500,2						479,9	
Silodach mit Dachhaube, mit Dachluke		Art.Nr.	4890000	4890100	4890200	4890300	4890300	4890500	4890000	4890100	4890200	4890300	4890400	4890500
		Höhe	1,08	1,36	1,59	1,85	1,85	2,37	1,08	1,36	1,59	1,85	2,11	2,37
		Vol	3,37	6,61	11,45	18,25	18,25	38,88	3,37	6,61	11,45	18,25	27,28	38,88
Belüftungskonus 27° Unterbau		Art.Nr.	3099000 normal	3099100 normal	3099200 normal	3099300 normal	3100100 normal	3100000 normal	3099400 erhöht + 0,6m	3099500 erhöht + 0,6m	3099600 erhöht + 0,6m	3099700 erhöht + 0,6m	3100110 erhöht + 0,6m	3100010 erhöht + 0,6m
Trichterhöhe	[m]		0,81	1,04	1,26	1,49	1,69	1,91	1,45	1,68	1,9	2,13	2,35	2,58
Mindervolumen	[m³]		5	11	19	31	45	66	12	21	33	50	72	98
Minderinhalt	[t]		3,8	8	14	23	34	48	9	16	25	38	54	74

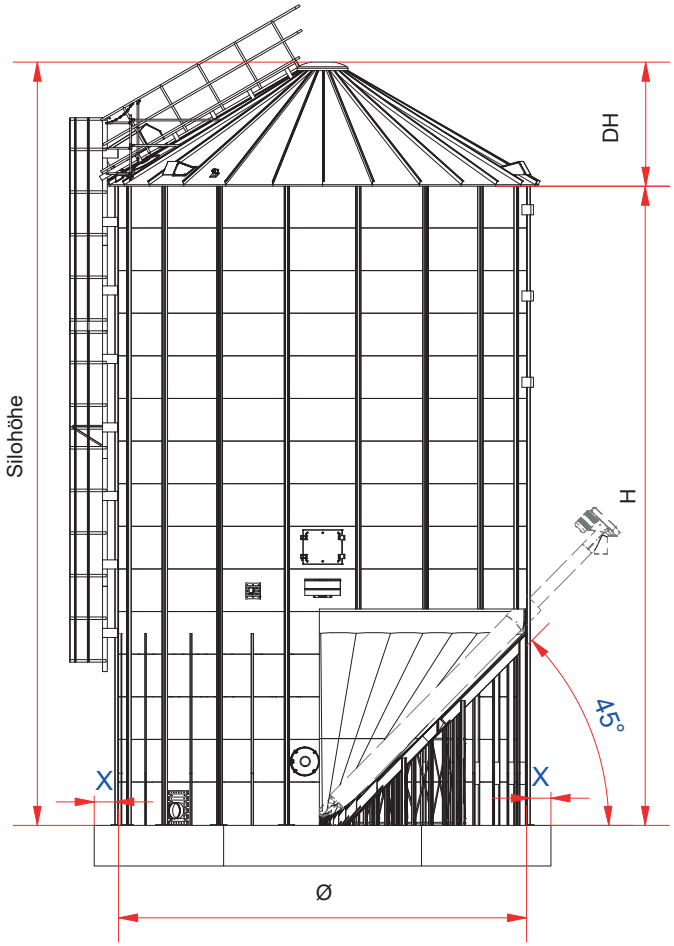


normaler Unterbau 45°

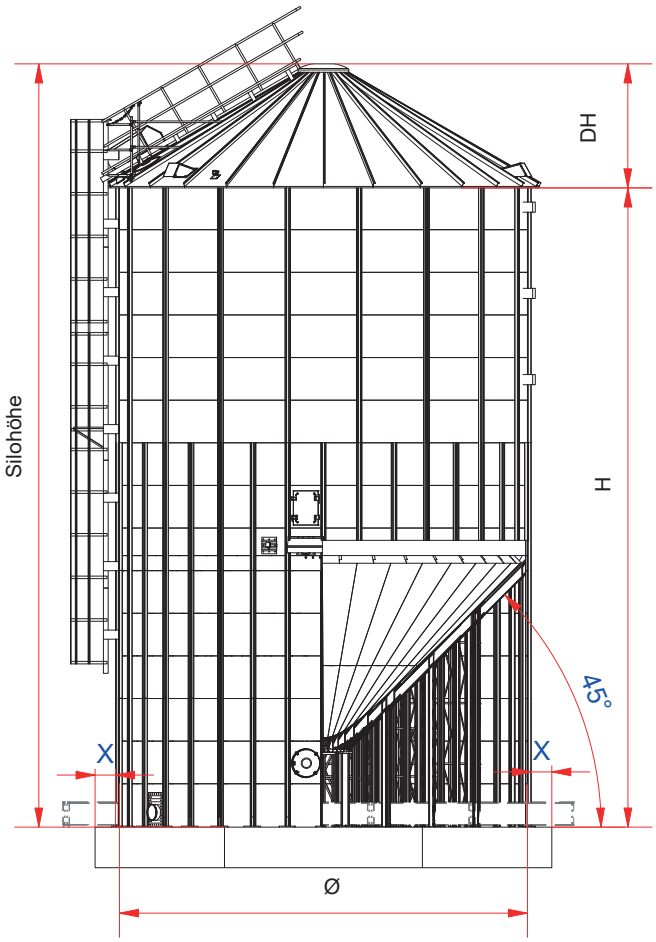

erhöhter Unterbau 45°

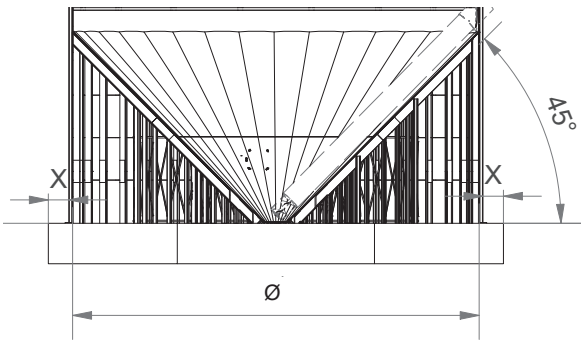

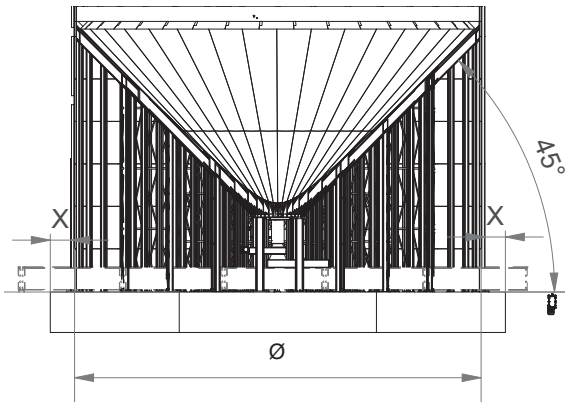

Lagersilo NLK 45° - Konus


Lagersilo NLK mit Stützen, für Belüftungskonus 45° normal + erhöht Innen-/Außenaufstellung, verzinkte Siloplatten mit flacher Profilierung, verzinkte C-Stützen, feuerverzinkte Verschraubung


Ringe	Zylinderhöhe Unterbau	Typ	NLK 4 normal	NLK 5 normal	NLK 6 normal	NLK 4 erhöht	NLK 5 erhöht	NLK 6 erhöt
[Anzahl]	[m]	Ø	3,58	4,47	5,36	3,58	4,47	5,36
5	**4,29**	Art.Nr.	4867400	4867500	4867610	4867400	4867500	4867610
		[m³]	32,2	46,3	59,8	26,2	36,3	44,8
		[t]	24,1	34,7	44,9	19,6	27,2	33,6
6	**5,13**	Art.Nr.	4867405	4867505	4867615	4867405	4867505	4867615
		[m³]	40,6	59,5	78,7	34,6	49,5	63,7
		[t]	30,5	44,6	59,1	26,0	37,1	47,8
7	**5,97**	Art.Nr.	4867410	4867510	4867620	4867410	4867510	4867620
		[m³]	49,1	72,7	97,7	43,1	62,7	82,7
		[t]	36,8	54,5	73,3	32,3	47,0	62,0
8	**6,81**	Art.Nr.	4867415	4867515	4867625	4867415	4867515	4867625
		[m³]	57,5	85,9	116,6	51,5	75,9	101,6
		[t]	43,2	64,4	87,5	38,7	56,9	76,2
9	**7,65**	Art.Nr.	4867420	4867520	4867630	4867420	4867520	4867630
		[m³]	66,0	99,1	135,5	60,0	89,1	120,5
		[t]	49,5	74,3	101,7	45,0	66,8	90,4
10	**8,49**	Art.Nr.	4867425	4867525	4867635	4867425	4867525	4867635
		[m³]	74,5	112,2	154,6	68,5	102,2	139,6
		[t]	55,8	84,2	116,0	51,3	76,7	104,7
11	**9,33**	Art.Nr.	4867430	4867530	4867640	4867430	4867530	4867640
		[m³]	82,9	125,4	173,5	76,9	115,4	158,5
		[t]	62,2	94,1	130,2	57,7	86,6	118,9
12	**10,17**	Art.Nr.	4867435	4867535	4867645	4867435	4867535	4867645
		[m³]	91,4	138,6	192,6	85,4	128,6	177,6
		[t]	68,5	103,9	144,5	64,0	96,4	133,2
13	**11,01**	Art.Nr.	4867440	4867540	4867650	4867440	4867540	4867650
		[m³]	99,8	151,8	211,4	93,8	141,8	196,4
		[t]	74,9	113,8	158,6	70,4	106,3	147,3
14	**11,85**	Art.Nr.	4867445	4867545	4867655	4867445	4867545	4867655
		[m³]	108,3	165,0	230,3	102,3	155,0	215,3
		[t]	81,2	123,7	172,8	76,7	116,2	161,5
15	**12,69**	Art.Nr.	4867450	4867550	4867660	4867450	4867550	4867660
		[m³]	116,7	178,1	249,3	110,7	168,1	234,3
		[t]	87,6	133,6	187,0	83,1	126,1	175,7
Silodach mit Dachhaube, mit Dachluke		Art.Nr.	4890000	4890100	4890200	4890000	4890100	4890200
		Höhe	1,08	1,36	1,59	1,08	1,36	1,59
		Vol	3,37	6,61	11,45	3,37	6,61	11,45
Belüftungskonus 45°		Art.Nr.	3099010	3099110	3099210	3099015	3099115	3099215
Unterbau			normal	normal	normal	erhöht + 0,6 m	erhöht + 0,6 m	erhöht + 0,6 m
Trichterhöhe	[m]		1,59	2,04	2,45	2,23	2,68	3,12
Mindervolumen	[m³]		11	21	37	17	31	52
Minderinhalt	[t]		8	16	28	13	23	39


Zubehör NLK

Zubehör	Typ	NLK 4	NLK 5	NLK 6	NLK 7	NLK 8	NLK 9
Dachverstärkung							
Dachverstärkung für den Einbau einer Temperaturmessanlage	Art.Nr.	4870000	4870100	4870200	4870250	4870300	4870450
Dachverstärkung für den Einbau einer Temperaturmeßanlage f. NL 9 ab 26 Ringe	Art.Nr.	-	-	-	-	-	4870460
Dachverstärkung für den Einbau einer Temperaturmeßanlage f. NL 10 ab 22 Ringe	Art.Nr.	-	-	-	-	-	-
Dachverstärkung für den Einbau einer Temperaturmessanlage f.NL 11 ab 19 Ringe	Art.Nr.	-	-	-	-	-	-
Dachleitern							
Dachleiter mit Geländer für NL	Art.Nr.	4899110	4899120	4899130	4899140	4899150	4899160
Sicherheitsverstrebung für Inspektionsluke	Art.Nr.	4958200					
Befüllstutzen							
Befüllstutzen Ø 150 = GUMA DS Verbindung	Art.Nr.	4958400					
Befüllstutzen Ø 150 = Spannring Verbindung	Art.Nr.	4958450					
Befüllstutzen Ø 150 = FS- Verbindung	Art.Nr.	4958500					
Dichtung für FS - Verbindung	Art.Nr.	0040227					
Befüllstutzen Ø 200 = Spannring Verbindung	Art.Nr.	4958550					
Befüllstutzen Ø 250 = Spannring Verbindung	Art.Nr.	4958700					
Dachhaube ND für NL 3-11 Einlauf Ø 300 mm, mit Befüllstutzen	Art.Nr.	4881115					
Dachentlüftung							
Entlüftungshaube 300x300mm für Silodach NL	Art.Nr.	4958330					
Dachentlüftungsgebläse NDE für NL-Silos mit Neigung 30° bzw. 25° bestehend aus: verzinkter Abdeckhaube, Lüfter mit Motor 0,55 kW EX - ATEX 21, Luftleistung freiblasend 7.400 m³/h	Art.Nr.	5302800					
Entnahmetechnik oberflur (Entnahmerohr)							
Entnahmerohre Gr. 310 mit Luke	Art.Nr.	3448202	3448302	3448402	3448502	3448602	3448702
Kappe Entnahmerohrmuffe Ø 310, außen 323,9 mm, verschraubbar, mit Montagepaket	Art.Nr.	4918000					
Entnahmerohrluke Gr. 400	Art.Nr.	3451000	3451010		3451020		
Für eine komplette Siloentnahme werden Entnahmerohrluke, Entnahmerohr und Abdeckhaube benötigt.							
Entnahmerohr Ø 400, 6 m lang, lackiert, 6,3 mm stark **(Länge ist bauseits anzupassen)**	Art.Nr.	4922000					
Entnahmerohrunterbauten für NL für Ø 310 und Ø 400	Art.Nr.	-	4923204		4923206		
Abdeckhaube S200, für Entnahmerohrluke Ø 400	Art.Nr.	8140900					
Abdeckhaube S250, für Entnahmerohrluke Ø 400	Art.Nr.	8140700					
Abdeckhaube S300, für Entnahmerohrluke Ø 400	Art.Nr.	7013643					
Rohrschutzkappe für Entnahmerohrmuffe Ø 400 (Rohrschutzkappe flexibel Ø 419 x 90)	Art.Nr.	8210980					
Abdeckhaube S300, für Entnahmerohrluke Ø 500	Art.Nr.	7002993					
Entnahmerohr Ø 500, 6 m lang, lackiert, 6,3 mm stark **(Länge ist bauseits anzupassen)**	Art.Nr.	-	-	-	4922100	-	-
Messstutzen und Vollmelder							
Messstutzen NL mit Schutzkappe und Torro-Schelle	Art.Nr.	4915500					
Messstutzen für Rundsilo NL mit Gewinde und Schraubkappe	Art.Nr.	7001025					
Drehflügelmelder mit Kunststoffflügel und 75 mm Welle, 230 V AC	Art.Nr.	3459000					
Drehflügelmelder mit Kunststoffflügel und 75 mm Welle, 24 V DC	Art.Nr.	3459150					
Bausatz für Pendelwelle L=500 mm	Art.Nr.	3459160					
Bausatz für Pendelwelle L=1000 mm	Art.Nr.	3459170					
Bausatz Seilverlängerung 2 m	Art.Nr.	3459180					
Einbaustutzen Drehflügelmelder am Silozylinder	Art.Nr.	3459800					
Einbaustutzen Drehflügelmelder am Silodach (30°)	Art.Nr.	3459500					
Einstiegluken							
Einstiegluke Ø 560 rund	Art.Nr.	3450530		3450540		3450550	
Einstiegluke eckig 700 x 600 mm, mit Einsetzlamellen	Art.Nr.	3446000		3446010			3446020
Einstiegluke eckig für doppelte Stützenreihe	Art.Nr.	3445606		3445605			3445705
Notauslauf Ø200 45° NL-Silo - verzinkt - **Nur zur kontrollierten Restentleerung!**	Art.Nr.	3457800					
Einstiegsgriff für Einstiegsluke	Art.Nr.	4881160					
Einstieghilfe zweistufig für NL-Silo, vormontiert	Art.Nr.	3420080					
Einstiegstufe dreistufig, für NL-Silo	Art.Nr.	3420085					
Wartungsbühne für NL-Silo, komplett	Art.Nr.	3420260					
Unterflurbelüftung							
Unterflurbelüftung bestehend aus Verschalungen, Kiemenplatten light B=300mm, Winkel, T-Stück und Enddeckel. **KG-Rohre zur Luftzufuhr sind bauseitig beizustellen.**	Art.Nr.	3884000	3884100	3884200	3884300	3884400	3884500
Siloanschlussstutzen Ø 310, NL	Art.Nr.	8210980					
Rohrschutzkappe Ø 310, innen 313 mm, für Rohr Ø 310, Rohrschellenverbindung	Art.Nr.	3099900	3099910	3099920	3099930	3100200	3100300
Auslaufschieber							
Schieber 200x200 elektrisch	Art.Nr.	4495100					
Schieber 250x250 elektrisch	Art.Nr.	4495000					
Schieber 250x250 fernbetätigt	Art.Nr.	4495010					
Schieber 250x250 handbetätigt	Art.Nr.	4495020					
Schieber 250x250 pneumatisch	Art.Nr.	1768540					
Schieber 300x300 elektrisch	Art.Nr.	4495040					
Schieber 300x300 fernbetätigt	Art.Nr.	4495050					
Schieber 300x300 handb Endschalt	Art.Nr.	4495080					
Schieber 300x300 handbetätigt	Art.Nr.	4495060					
Schieber 300x300 pneumatisch	Art.Nr.	4495070					

Lagersilo NLT 36°/45°/60° mit Stützen

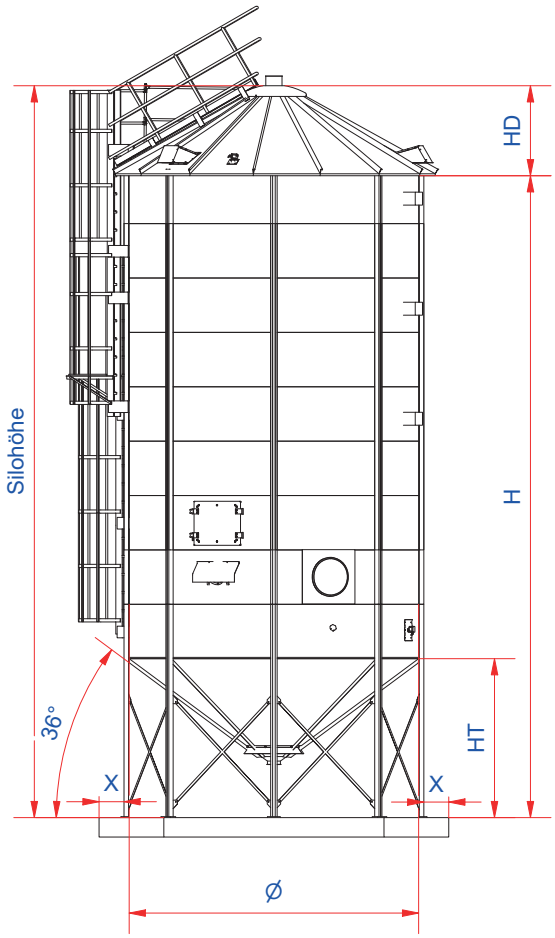

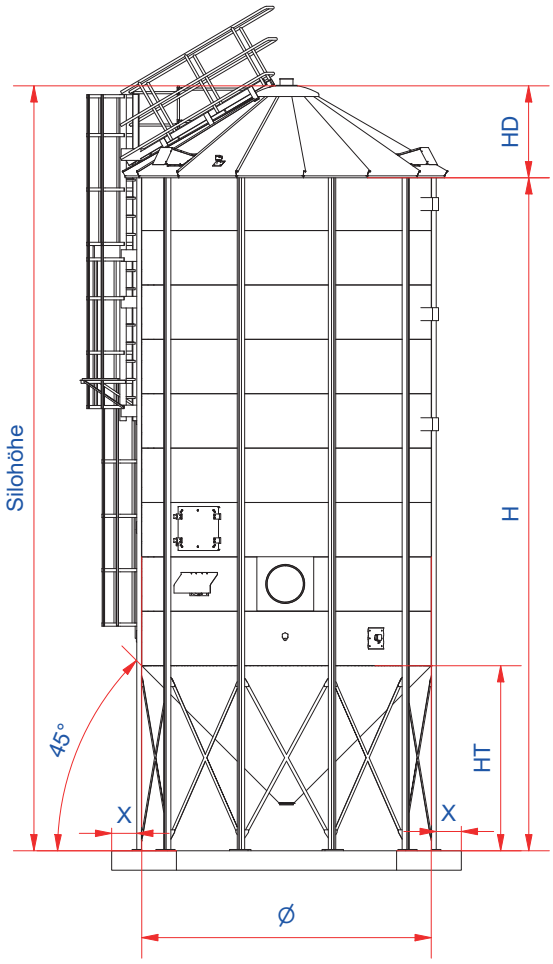

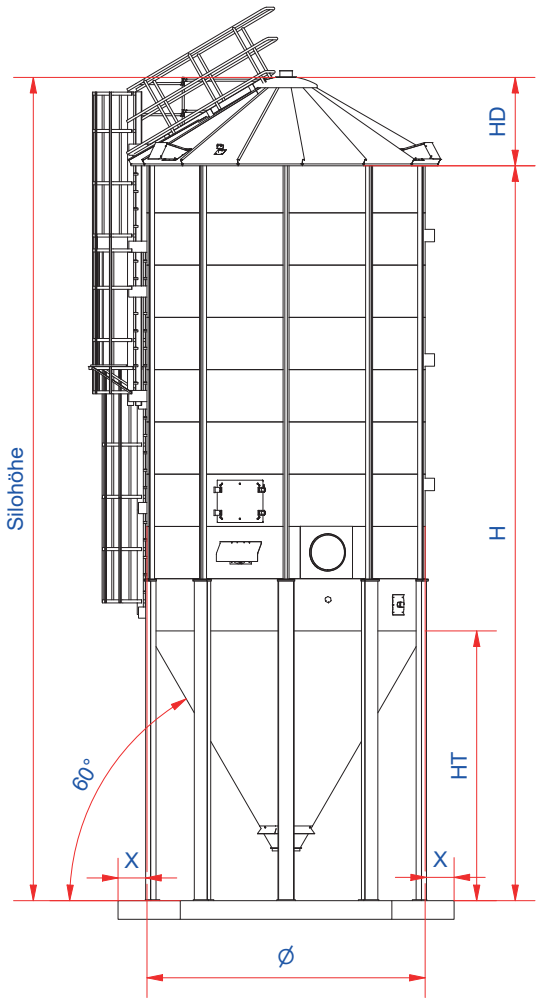

Lagersilo NLT 36°/45°/60° mit Stützen

Lagersilo NLT, 36°/45°/60° Trichter, mit Stützen Innen- und Außenaufstellung, verzinkt, Trichtersegmente, Trichterstützen, Stützenstreben, C-Stützen, Siloplatten mit flacher Profilierung

Ringe	Typ	**NLT 2**	**NLT 3**	**NLT 4**	**NLT 5**	**NLT 3**	**NLT 4**	**NLT 5**	**NLT 6**	**NLT 5**
Trichterneigung	°	36	36	36	36	45	45	45	45	60
inkl. Trichtervolumen von	[m³]	0,5	1,8	4,4	8,5	2,5	6,0	11,7	20,2	20,2
Höhe Unterbau	m	1,3	1,66	2,02	2,38	2,02	2,50	2,86	3,33	4,56
[Anzahl]	Ø	1,79	2,68	3,58	4,47	2,68	3,58	4,47	5,36	4,47
3	Höhe	3,91	4,27	4,63	4,99	4,63	5,11	5,47	5,94	7,1
	Art.Nr.	4701501	4706501	4712501	4718501	4740000	4741000	4742000	4743000	4741130
	[m³]	7,1	16,6	30,6	49,5	17,2	32,3	52,6	79,0	61,2
	[t]	5,3	12,4	23,0	37,1	12,9	24,2	39,5	59,3	45,9
4	Höhe	4,75	5,11	5,47	5,83	5,47	5,95	6,31	6,78	7,94
	Art.Nr.	4701701	4706701	4712701	4718701	4740010	4741010	4742010	4743010	4741140
	[m³]	9,2	21,3	36,6	56,0	22,0	40,7	60,1	83,9	74,4
	[t]	6,9	16,0	27,4	42,0	16,5	30,6	45,1	62,9	55,8
5	Höhe	5,59	5,95	6,31	6,67	6,31	6,79	7,15	7,62	8,78
	Art.Nr.	4701901	4706901	4712901	4718901	4740020	4741020	4742020	4743020	4741150
	[m³]	11,3	26,0	45,0	69,2	26,7	49,2	73,3	102,8	87,6
	[t]	8,5	19,5	33,8	51,9	20,0	36,9	55,0	77,1	65,7
6	Höhe	6,43	6,79	7,15	7,51	7,15	7,63	7,99	8,46	9,62
	Art.Nr.	4702101	4707101	4713101	4719101	4740030	4741030	4742030	4743030	4741160
	[m³]	13,5	30,8	56,0	89,0	31,5	57,6	92,2	135,9	100,7
	[t]	10,1	23,1	42,0	66,7	23,6	43,2	69,1	101,9	75,5
7	Höhe	7,27	7,63	7,99	8,35	7,99	8,47	8,83	9,3	10,46
	Art.Nr.	4702301	4707401	4713301	4719301	4740040	4741040	4742040	4743040	4741170
	[m³]	15,6	35,5	64,5	102,2	36,2	66,1	105,4	154,9	113,9
	[t]	11,7	26,6	48,3	76,6	27,1	49,6	79,0	116,1	85,4
8	Höhe	8,11	8,47	8,83	9,19	8,83	9,31	9,67	10,14	11,3
	Art.Nr.	4702501	4707501	4713501	4719501	4740050	4741050	4742050	4743050	4741180
	[m³]	17,7	40,2	72,9	115,4	40,9	74,6	118,6	173,8	127,1
	[t]	13,3	30,2	54,7	86,5	30,7	55,9	88,9	130,4	95,3
9	Höhe	8,95	9,31	9,67	10,03	9,67	10,15	10,51	10,98	12,14
	Art.Nr.	4702701	4707701	4713701	4719701	4740060	4741060	4742060	4743060	4741190
	[m³]	19,8	45,0	81,4	128,5	45,7	83,0	131,7	192,8	140,3
	[t]	14,8	33,7	61,0	96,4	34,3	62,3	98,8	144,6	105,2
Silodach mit Dachhaube, mit Dachluke	Art.Nr.	4899980	4889900	4890000	4890100	4889900	4890000	4890100	4890200	4890100
	Höhe	0,5	0,72	1,08	1,36	0,72	1,08	1,36	1,59	1,36
	Vol	0,4	1,41	3,37	6,61	1,41	3,37	6,61	11,45	6,61

weitere Größen auf Anfrage


Lagersilo NLT Zubehör

Zubehör		NLT 2	NLT 3	NLT 4	NLT 5	NLT 6
Dachleiter						
Dachleiter mit Geländer für NL	**Art.Nr.**	-	4899100	4899110	4899120	4899130
Befüllstutzen						
Befüllstutzen Ø 150mm mit Guma-DS-Vebindung	**Art.Nr.**		4958400			
Befüllstutzen Ø 150mm mit Spannring-Vebindung	**Art.Nr.**		4958450			
Befüllstutzen Ø 150mm mit FS Verbindung	**Art.Nr.**		4958500			
Dichtung für FS-Verbindung Ø150mm	**Art.Nr.**		0040227			
Befüllstutzen Ø 200mm mit Spannring-Vebindung	**Art.Nr.**		4958550			
Befüllstutzen Ø 250mm mit Spannring-Vebindung	**Art.Nr.**		4958700			
Dachhaube Ø 300 mit Befüllstutzen	**Art.Nr.**		4881115			
Einstiegluken						
Einstiegluke Ø560 rund	**Art.Nr.**	3450490	3450530	3450530	3450540	
Dachentlüftung						
Dachentlüftungsgebläse NDE, 0,42 kW EX-ATEX 21	**Art.Nr.**		5302800			
Entlüftungshaube 300mmx300mm für Silodach	**Art.Nr.**		4958330			
Messstutzen und Vollmelder						
Drehflügelmelder mit Kunststoffflügel und 75mm Welle, 230V AC	**Art.Nr.**		3459000			
Drehflügelmelder mit Kunststoffflügel und 75mm Welle, 24V DC	**Art.Nr.**		3459150			
Bausatz für Pendelwelle L=500mm	**Art.Nr.**		3459160			
Bausatz für Pendelwelle L=1000mm	**Art.Nr.**		3459170			
Bausatz Seilverlängerung 2m	**Art.Nr.**		3459180			
Einbaustutzen Drehflügelmelder am Silodach (30°)	**Art.Nr.**		3459500			
Messstutzen mit Kunststoffkappe + Normaschelle	**Art.Nr.**		4915500			
Messstutzen für Rundsilo mit Gewinde und Schutzkappe	**Art.Nr.**		7001025			
Einbaustutzen Drehflügelmelder am Silozylinder	**Art.Nr.**		3459800			
Einbaustutzen Drehflügelmelder am Silodach	**Art.Nr.**		3459500			
Auslaufklappen						
Auslaufklappe Ø 200mm für Raps 36°	**Art.Nr.**	4932250	4932350	4932450	4932550	-
Auslaufklappe Ø 200mm für Raps 45°	**Art.Nr.**	-	4932650	4932750	4932850	4932650
Regenkragen Auslauf 36°	**Art.Nr.**	4932910	4932920	4932920	4932940	
Regenkragen Auslauf 45°	**Art.Nr.**	**4932925**		**4932935**		
Belüftungseinrichtung						
Belüftungseinrichtung Ø 150, 36° Trichter, Getreide	**Art.Nr.**	3879200	3879300	-	-	-
Belüftungseinrichtung Ø 150, 45° Trichter, Getreide	**Art.Nr.**	-	3879350	-	-	-
Belüftungseinrichtung Ø 150, 36° Trichter, Raps	**Art.Nr.**	-	3879310	-	-	-
Belüftungseinrichtung Ø 150, 45° Trichter, Raps	**Art.Nr.**	-	3879741	-	-	-
Belüftungseinrichtung Ø 300, 36° Trichter, Getreide	**Art.Nr.**	-	-	3879700	3879720	-
Belüftungseinrichtung Ø 300, 45° Trichter, Getreide	**Art.Nr.**	-	-	3879710	3879730	3879740
Belüftungseinrichtung Ø 300, 36° Trichter, Raps	**Art.Nr.**	-	-	3879745	3879755	-
Belüftungseinrichtung Ø 300, 45° Trichter, Raps	**Art.Nr.**	-	-	3879750	3879760	3879770


Belüftungseinrichtungen

Belüftungseinrichtungen für runde Lagersilos - Belüftungskanäle -


Belüftungseinrichtung D150/D310, bestehend aus: Siloanschlussstutzen mit Verschlussdeckel, Belüftungskanäle voll gelocht, Verteiler und Befestigungsmaterial				
Silotyp	**Anz. Ringe**	**Silo Ø**	**Anschluß**	**Art.-Nr.**
NLI 2	3-10	2,24m	Ø 150	3882200
NLI 3	3-10	2,68m	Ø 150	3882200
NLI 3.5	3-10	3,13m	Ø 150	3882200
NLI 4	3-10	3,58m	Ø 150	3882200
NLI 4.5	3-10	4,02m	Ø 150	3882300
NLI 5	5-10	4,47m	Ø 150	3882300
NLI 5.5	5-9	4,92m	Ø 310	3882900
NLI 6	5-9	5,36m	Ø 310	3882900
NLI 7	5-9	6,26m	Ø 310	3883100
Belüftungseinrichtung D150/D310, bestehend aus: Siloanschlussstutzen mit Verschlussdeckel, Belüftungskanäle voll gelocht, Verteiler und Befestigungsmaterial				
Silotyp	**Anz. Ringe**	**Silo Ø**	**Anschluß**	**Art.-Nr.**
NL 3	3-15	2,68m	Ø 150	3882200
NL 4	3-12	3,58m	Ø 150	3882200
NL 5	5-10	4,47m	Ø 150	3882300
NL 4	13-20	3,58m	Ø 310	3882500
NL 5	11-22	4,47m	Ø 310	3882800
NL 6	5-22	5,36m	Ø 310	3883100
NL 7	5-22	6,26m	Ø 310	3883110
NL 8	7-24	7,15m	Ø 310	3883130
NL 9	7-24	8,04m	Ø 310	3883140
NL10	7-23	8,94m	Ø 310	3883150

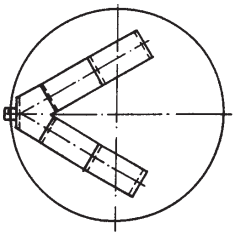

bis NL 7/10

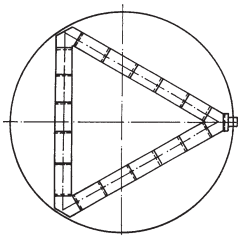


ab NL 7/11 + 8

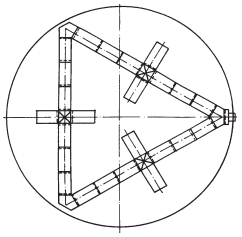

für NL 9 + 10

Einzelbauteile Belüftungseinrichtung		Art.-Nr.
Siloanschluss-Stutzen Ø 150 (Blech gewellt)		3457500
Siloanschluss-Stutzen Ø 150 (Blech glatt)		3456501
Gummideckel Ø 150		0042560
Siloanschluss-Stutzen Ø 310 (Blech gewellt)	**(1)**	3457600
Belüftungsschlauch 1 mtr.	**(3)**	0046541
Enddeckel für Schlauch		3456535
Verbindungsmuffe für Schlauch		3453900
Schlauchführung gerade	**(2)**	3456531
Schlauchführung 90 Grad	**(5)**	3456532
Belüftungs-T-Stück Ø 150	**(6)**	3456504
Belüftungskreuz Ø 150	**(4)**	3456505
Belüftungskreuz Ø 310/150		3458000

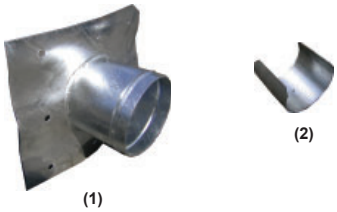

(1)


(2)



(3)



(4)

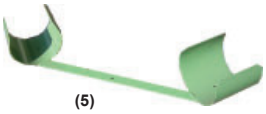

(5)


Einzelbauteile für Belüftungseinrichtung:		Art.-Nr.
Belüftungskanal 24/48 voll gelocht, 0,9 m lang	**(8)**	0044178
Belüftungskanal 24/48 teil gelocht, 0,9 m lang		3453800
Belüftungskanal 24/48 voll gelocht, 0,9 m lang, für Raps		3453850
Y-Verteiler für Belüftungskanal 24/48	**(7)**	3457910
Y-Verteiler 90° für Belüftungskanal 24/48		3457920
Kreuzverteiler für Belüftungskanal 24/48		3453803
Winkel 90° für Belüftungskanal 24/48		3453804
Endplatte für Belüftungskanal 24/48		3453806
Belüftungskanal 32/64 voll gelocht	**(8)**	0044179
Kreuzverteiler 32/64	**(9)**	3453802
Endplatte 32/64		0044185
Gebläseanschluss 310 32/64		0044180
Gebläseanschluss Ø150, NL,mit Anschlussplatte u. Dichtung f. 24/48		3457510
Gebläseanschluss Ø310, NL, mit Anschlussplatte gewellt u. Dichtung f. 24/48		3457610
Gebläseanschluss Ø310, NLR, mit Anschlussplatte glatt u. Dichtung f. 24/48		3457615
Gummideckel Ø150 = Verschlussdeckel		0042560
Verschlussdeckel Kunststoff für Gebläse-Anschluss 310/300		3459510
Abdeckplatte für Siloanschlußstutzen Ø310		5302449
Düsenblech 1,25 x 1000 x 2000, 0,9mm Lochöffnung, verzinkt		4989000



(6)



(7)

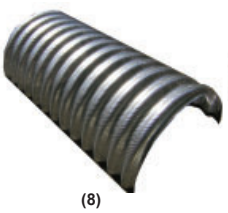


(8)



(9)

Belüftungseinrichtungen

Belüftungsplatte Typ HD
befahrbare Radlast max 10 to gemäß Brückenlast 60/30 DIN 1072a DIN EN 1991-2 für Unterflurbelüftung in Flachlagern mit Verstärkungsträgern. Für Luftbereifung geeignet, bei Verwendung von nicht luftbereiften Rädern kann es zu Verformungen kommen.

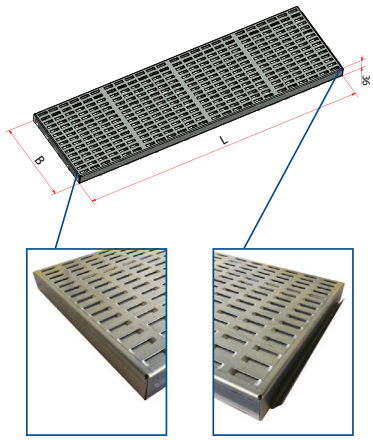

Deckbreite, Höhe, Stärke 300 mm/36 mm/1,5 mm
Belüftungsfläche in % 29,00 %


Typ	Breite mm	Länge mm	Art.-Nr.
HD 10to	300	250	4999861
HD 10to	300	500	4999811
HD 10to	300	1000	4999801

Belüftungsplatte Typ L300/500/800
für Unterflurbelüftung, für Schütthöhen bis 25 m bei einem Schüttgewicht von 750 kg/m³ **nicht befahrbar**

Deckbreite, Höhe, Stärke 300/500/800 mm/36 mm/1,5 mm
Belüftungsfläche in % 29,00 %
Schlitzbrücken rapstauglich ≤1,35 mm

Länge	Breite	Art.-Nr.	Breite	Art.-Nr.	Breite	Art.-Nr.
250	300	4999851	500	4999871	800	4999751
500	300	4999841	500	4999881	800	4999761
1000	300	4999831	500	4999850	800	4999771
2000	300	4999821	500	4999891	-	-

Lochblechabdeckung Typ HD
befahrbare Radlast max 10 to gemäß Brückenlast 60/30 DIN 1072a DIN EN 1991-2 für Unterflurbelüftung in Flachlagern mit Verstärkungsträgern. Für Luftbereifung geeignet, bei Verwendung von nicht luftbereiften Rädern kann es zu Verformungen kommen.

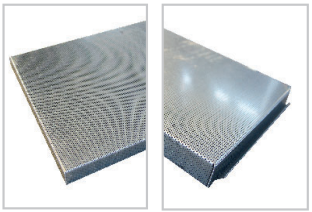


Bundesrepublik Deutschland

Urkunde

über die Erteilung des
Patents Nr. 10 2016 121 365

Bezeichnung:
Vorrichtung zur Lagerung von Getreide mit Belüftungsplatte

IPC:
A01F 25/14

Inhaber/Inhaberin:
NEUERO Farm- und Fördertechnik Gesellschaft mit beschränkter Haftung,
49328 Melle, DE

Erfinder/Erfinderin:
Hemmen, Markus, 32257 Bünde, DE

Tag der Anmeldung:
08.11.2016

Tag der Veröffentlichung der Patenterteilung:
29.03.2018

Die Präsidentin des Deutschen Patent- und Markenamts

Cornelia Rudloff-Schäffer

München, 29.03.2018

Den aktuellen Rechtsstand und Schutzumfang entnehmen Sie bitte dem DPMAregister unter www.dpma.de.

Deckbreite, Höhe, Stärke 300 mm/36 mm/1,5 mm
Lochgröße 1,5 mm
Luftdruchlassfläche in % 22,7 % (nach ISO)


Typ	Breite mm	Länge mm	Art.-Nr.
HD 10to	300	250	4999865
HD 10to	300	500	4999815
HD 10to	300	1000	4999805

Lochblechabdeckung Typ L300/500/800
für Unterflurbelüftung, für Schütthöhen bis 25 m bei einem Schüttgewicht von 750 kg/m³ **nicht befahrbar**


Deckbreite, Höhe, Stärke 300/500/800 mm/36 mm/1,5 mm
Lochgröße 1,5 mm
Luftdruchlassfläche in % 22,7 % (nach ISO)

Länge	Breite	Art.-Nr.	Breite	Art.-Nr.	Breite	Art.-Nr.
250	300	4999855	500	4999875	800	4999755
500	300	4999845	500	4999885	800	4999765
1000	300	4999835	500	4999856	800	4999775
2000	300	4999825	500	4999895	-	-


Verlorene Schalung:	Art.-Nr.
Verlorene Schalung B=300, L=2000 mm, verzinkt, 1mm Blechstärke	4999620
Verlorene Schalung B=300, L=1000 mm, verzinkt, 1mm Blechstärke	4999622
Verlorene Schalung B=300, L= 500 mm, verzinkt, 1 mm Blechstärke	4999623
Kreuzstück verlorene Schalung	4999660
Enddeckel B=300mm, verlorene Schalung, verzinkt	4999630
Winkel 90° rechts B=300 mm, verlorene Schalung, verzinkt, 1 mm Blech	4999640
Winkel 90° links B=300 mm, verlorene Schalung, verzinkt, 1 mm Blech	4999645
T-Stück B=300 mm, verlorene Schalung, verzinkt, 1 mm Blech*	4999650

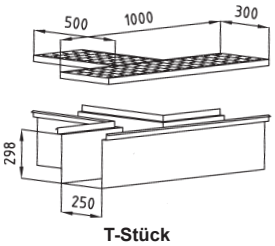


T-Stück

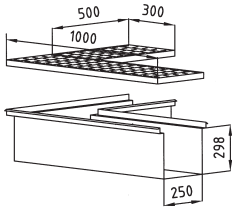


Winkel 90° links/rechts

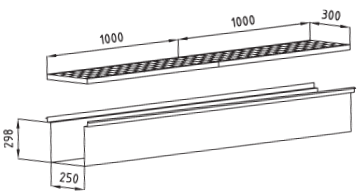

Verlorene Schalung

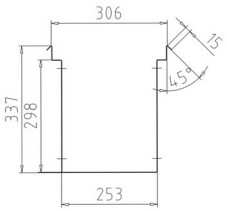

Verlorene Schalung Querschnitt

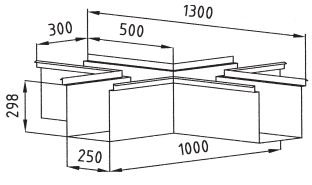

Kreuzstück

Belüftungseinrichtungen

Der Belüftungsspeer klimatisiert das Getreide im Umkreis und wird einfach versetzt. So wird das Getreide sukzessive belüftet.

Vorteile:

- schützt mit wenig Aufwand vor hohen Verlusten
- beseitigt auftretende Hitzenester im Getreide
- wird einfach in das Getreide gesteckt, anschließend mit dem Handgriff in die Tiefe gedreht und ist dann betriebsbereit



Spiral
Ø 200 mm

	Belüftungsspeer, 230 V	Belüftungsspeer, 380 V
Motorleistung	150 W	2,2 kW
	nur saugend	saugend und blasend
Luftleistung	250 m ³/h	2500 m ³/h
Gesamtlänge	2,5 m	3,0 - 3,8 m, teleskopierbar
Belüftungsstück perforiert	0,8 m	1,5 m
nicht perforierte Rohrlänge	1,2 m	0,5 - 1,3 m
Einsteckspitze	0,25 m	0,25 m
Gewicht ca.	13,0 kg	36 kg
Perforation 1,5 mm	(auch für Raps)	(auch für Raps)

Typ	Art.-Nr.
Belüftungsspeer mit Ventilator 150W 230V	3432000
Belüftungsspeer ohne Ventilator	3432100
Belüftungsspeer mit Ventilator 2,2 kW 380V	3433000
Belüftungsspeer ohne Ventilator	3433100

**zzgl. Verpackungskosten pro Teleskop-Belüftungsspeer zzgl. MWSt

Der Belüftungsspeer (230 V) arbeitet saugend.
Der Belüftungsspeer (380 V) kann sowohl saugend als auch blasend (durch Umsetzen des Gebläses) eingesetzt werden.

Verzinktes Teleskop-Belüftungsrohr


Typ	Anzahl der Rohre	Länge Einzelrohr m	Nennlänge	Anschluss-stutzen Ø mm	Gewicht kg	ausgezogene Nutzlänge ca. m	Art.-Nr.
2/2/4/300	2	2	4	300	42	3,92	3430305
3/2/6/300	3	2	6	300	60	5,85	3430315
4/2/8/300	4	2	8	300	75	7,77	3430310
5/2/10/300	5	2	10	300	90	9,70	3430320
6/2/12/300	6	2	12	300	103	11,62	3430300
7/2/14/300	7	2	14	300	117	13,55	3430325
8/2/16/300	8	2	16	300	129	15,47	3430330
9/2/18/300	9	2	18	300	140	17,40	3430335
10/2/20/300	10	2	20	300	150	19,32	3430340
Silodurchführung für Teleskopbelüftungsrohr zum Selbsteinbau in Silowände von 20 - 200 mm Wandstärke							3430350

- beschüttbar bis 5 m Höhe
- Luftaustrittsfläche auf die gesamte Länge 22 %
- gleichmäßige Luftverteilung entlang des Teleskoprohres
- jedes Einzelrohr besitzt die gleiche Luftaustrittsfläche
- geeignet für Flachlagerbelüftung
- Teleskop wird mechanisch aus dem vollem Getreidelager gezogen
- problemloses Auseinanderziehen des Rohrbündels durch Sicken, Flacheisen, Mitnehmer möglich
- Dichtungsmechanismus jedes einzelnen Rohres
- innenliegende Seilbefestigung
- leichte Erweiterbarkeit des Teleskoprohres durch modularer Aufbau möglich
- Lochung 1,5 mm, auch für Raps geeignet




Wanddurchführung 0,5 m (serienmäßig)




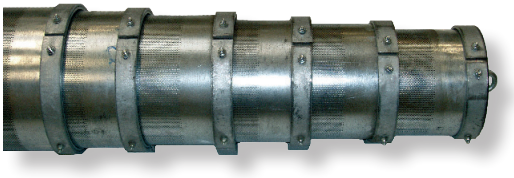


Verlegeabstand der Teleskopbelüftungsrohre

Schütthöhe	2 m	2,5 m	3 m	3,5 m	4 m	4,5 m	5 m
Abstand der Rohre	2 m	2,25 m	2,5 m	2,75 m	3 m	3,25 m	3,5 m

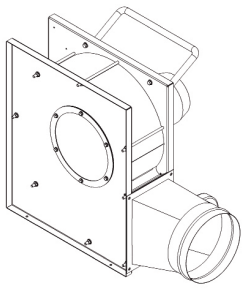

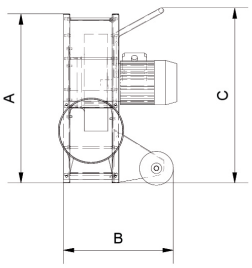

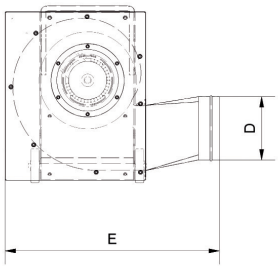

Typ	A	B	C	D	E
NV 11	575	463	743	150	782
NV 30	800	490	828	310	1.015
NV 35	800	490	828	310	1.015
NV 55 S	900	546	936	310	1.142
NV 75 HD	900	546	936	310/500	1.142


Alle Maße in mm

Ventilator **Typ**	**NV 11**	**NV 30**	**NV 35**	**NV 55 S**	**NV 75 HD**
Motor (400V, 50Hz) kW	1,1	3,0	4,0	5,5	7,5
Ventilator-Drehzahl min^{-1}	2.900	2.900	2.900	2.900	2.900
Luftleistung (m^3/h) Druck (Pa)	2000/920	4000/1180	5000/1200	7000/2100	6000/3000
Luftleistung (m^3/h) Druck (Pa) Ø 500					8000/2000
Ausblas Ø	150 mm	310 mm	310 mm	310 mm	310 mm/500 mm
Gewicht ca.	44 kg	64 kg	87 kg	105 kg	136 kg
	Art.-Nr.	**Art.-Nr.**	**Art.-Nr.**	**Art.-Nr.**	**Art.-Nr.**
Ventilator einschl. Fahrvorrichtung u. angebautem MSS+CEE-Stecker 16A	3129501	3129701	3129901	-	-
Ventilator einschl. Fahrvorrichtung Sterndreieckschalter mit MSS	-	-	-	3700015	3700026
Ausblasstutzen Ø 310				im Ventilatorpreis	3700325
Ausblasstutzen Ø 500	-	-	-	-	3700340
PVC-Schlauch Ø 520, 0,5 m lg.	-	-	-	-	8314000
Norma-Schelle Ø 500 (2 St. einplanen)	-	-		-	8314005

Zubehör

Spiralschläuche für Belüftungsventilator	**Art.-Nr.**
Spiralschlauch Ø 150, 1,0 m lang, mit 2 Schnallgurten	3457200
Spiralschlauch Ø 150, 2,0 m lang, mit 2 Schnallgurten	3457210
Spiralschlauch Ø 310, 1,0 m lang, mit 2 Schnallgurten	3457250
Spiralschlauch Ø 310, 2,0 m lang, mit 2 Schnallgurten	3457255
Spiralschlauch Ø 310, 3,0 m lang, mit 2 Schnallgurten	3457256
Spiralschlauch Ø 320/150, 1,5 m lang, mit Schnallgurt	3457270
Schallschutzhaube NV 30 - 75	3710300

Belüftungsschläuche für NLT Silos	**Art.-Nr.**
Belüftungsschlauch Ø 150, 2,8 m lg., für Gebläse NV 11 (f. NLT 2+3, 36 Grad)	3457350
Belüftungsschlauch Ø 150, 3,5 m lg., für Gebläse NV 11 (f. NLT 3, 45 Grad)	3457450
Spannring Ø 150, zweiteilig, 2 mm,mit Verschraubung verzinkt	0045939
Belüftungsschlauch Ø 310, 3,5 m lg., mit 2 Schnallgurten, für Gebläse NV 30 (f. NLT 4+5, 36 Grad)	3457475
Belüftungsschlauch Ø 310, 4,0 m lg., mit 2 Schnallgurten, für Gebläse NV 30 (f. NLT 4+5, 45 Grad)	3457480
Belüftungsschlauch Ø 310, 4,5 m lg., mit 2 Schnallgurten, für Gebläse NV 30 (f. NLT 6, 45 Grad)	3457485

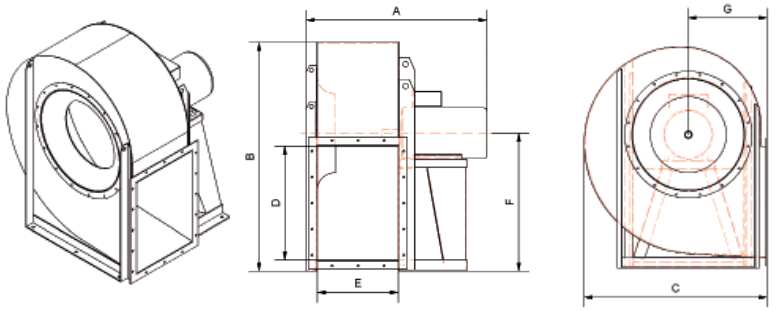

Typ	A	B	C	D	E	F	G
NV 40	779	1124	938	569	404	670	400
NV 55	885	1260	1050	640	455	750	450
NV 75	885	1260	1050	640	455	750	450
NV 110	1040	1415	1160	715	510	850	500
NV 150	1040	1415	1160	715	510	850	500
NV 185	1240	1590	1315	800	570	950	560
NV 220	1240	1590	1315	800	570	950	560

Standard-Ausführung: einseitig saugend, Ausblasstellung 270° (Einsatz auch um 90° versetzt möglich), Ansaugschutzgitter und Bodenkonsole.
***Alle Maße in mm** / Änderungen vorbehalten.*

Ventilator **Typ**	**NV 40**	**NV 55**	**NV 75**	**NV 110**
Motor N=1450min^{-1} kW (400V,50Hz), direkt gekuppelt	4,0	5,5	7,5	11,0
Luftleistung (m³/h) Druck (Pa)	7000/1100	10000/1200	17.500/1000	22.500/1250
Ausblas-Ø	500 mm	500/630mm	500/630 mm	630 mm
Gewicht ca.	175	210	235 kg	278 kg
	Art.-Nr.	**Art.-Nr.**	**Art.-Nr.**	**Art.-Nr.**
Ventilator	3710000	3710010	3710020	3710030
Sterndreieckschalter mit Motorschutzschalter und Einphasen-Netzabgang	0082654	0082654	0082656	0082657
Ausblasstutzen für Rohrschellenverbindung Ø 500	3710090	3710100	3710100	-
Ausblasstutzen für Rohrschellenverbindung Ø 630	-	3710110	3710110	3710120
Übergangsstück Ventilator/Warmlufterzeuger	3710095	3710200	3710200	3710210
Rohrschelle Ø630 mit Dichtung, zur Befestigung Ventilator/Warmlufterzeuger	8252800	8272600	8272600	8272600
Fahrvorrichtung	3701200	3701200	3701200	3701200

Ventilator **Typ**	**NV 150**	**NV 185**	**NV 220**
Motor N=1450min^{-1} kW (400V,50Hz), direkt gekuppelt	15,0	18,5	22,0
Luftleistung m³/h / Druck Pa	28500/1100	35000/1400	45000/1000
Ausblas-Ø	630 mm	630 mm	630 mm
Gewicht ca.	320 kg	420 kg	460 kg
	Art.-Nr.	**Art.-Nr.**	**Art.-Nr.**
Ventilator	3710040	3710050	3710060
Sterndreieckschalter mit Motorschutzschalter und Einphasen-Netzabgang	0082655	auf Anfrage	auf Anfrage
Ausblasstutzen für Rohrschellenverbindung Ø 500	-	-	-
Ausblasstutzen für Rohrschellenverbindung Ø 630	3710120	3710130	3710130
Übergangsstück Ventilator/Warmlufterzeuger	3710210	3710220	3710220
Rohrschelle Ø630 mit Dichtung, zur Befestigung Ventilator/Warmlufterzeuger	8272600	8272600	8272600
Fahrvorrichtung	3701200	3701200	3701200

Ventilatoren

Ringe	NL 2			NL 3			NL 4			NL 5			NL 6		
[Anzahl]	Typ Ventilator	Anzahl Dachhauben	Anzahl Dachentlüftungsgebläse	Typ Ventilator	Anzahl Dachhauben	Anzahl Dachentlüftungsgebläse	Typ Ventilator	Anzahl Dachhauben	Anzahl Dachentlüftungsgebläse	Typ Ventilatorlator	Anzahl Dachhauben	Anzahl Dachentlüftungsgebläse	Typ Ventilator	Anzahl Dachhauben	Anzahl Dachentlüftungsgebläse
1	NV11	1		NV11	1		NV11	1		NV11	1		NV30	1	
2	NV11	1		NV11	1		NV11	1		NV11	1		NV30	1	
3	NV11	1		NV11	1		NV11	1		NV11	1		NV30	1	
4	NV11	1		NV11	1		NV11	1		NV11	1		NV30	1	
5	NV11	1		NV11	1		NV11	1		NV11	1		NV30	1	
6	NV11	1		NV11	1		NV11	1		NV11	1		NV30	1	
7	NV11	1		NV11	1		NV11	1		NV11	1		NV30	1	
8	NV11	1		NV11	1		NV11	1		NV30	1		NV30	1	
9	NV11	1		NV11	1		NV11	1		NV30	1		NV30	1	
10	NV11	1		NV11	1		NV11	1		NV30	1		NV30	1	
11	NV11	1		NV11	1		NV30	1		NV30	1		NV35	2	
12	NV11	1		NV11	1		NV30	1		NV30	1		NV35	2	
13	NV11	1		NV11	1		NV30	1		NV30	1		NV35	2	
14	NV11	1		NV11	1		NV30	1		NV30	1		NV35	2	
15	NV11	1		NV11	1		NV30	1		NV30	1		NV35	2	
16	NV11	1		NV11	1		NV30	1		NV35	1		NV75 HD	3	
17	NV11	1		NV11	1		NV30	1		NV35	1		NV75 HD	3	
18	NV11	1		NV11	1		NV30	1		NV35	1		NV75 HD	3	
19	NV11	1		NV11	1		NV30	1		NV35	1		NV75 HD	3	
20	NV11	1		NV11	1		NV30	1		NV35	1		NV75 HD	3	
21	NV11	1		NV11	1					NV75 HD	1		NV75 HD	3	
23	NV11	1		NV11	1					NV75 HD	1		NV75 HD	3	
24	NV11	1		NV11	1					NV75 HD	1		NV75 HD	3	
25	NV11	1		NV11	1					NV75 HD	1		NV75 HD	3	
26															
27															
28															
29															
30															

Ventilatoren

Ringe	NL 7			NL 8			NL 9			NL 10		
[Anzahl]	Typ Ventilator	Anzahl Dachhauben	Anzahl Dachentlüftungsgebläse	Typ Ventilator	Anzahl Dachhauben	Anzahl Dachentlüftungsgebläse	Typ Ventilator	Anzahl Dachhauben	Anzahl Dachentlüftungsgebläse	Typ Ventilator	Anzahl Dachhauben	Anzahl Dachentlüftungsgebläse
1	NV30	1		NV35	2		NV55 S	2		2xNV55 S	5	
2	NV30	1		NV35	2		NV55 S	2		2xNV55 S	5	
3	NV30	1		NV35	2		NV55 S	2		2xNV55 S	5	
4	NV30	1		NV35	2		NV55 S	2		2xNV55 S	5	
5	NV30	1		NV35	2		NV55 S	2		2xNV55 S	5	
6	NV30	1		NV35	2		NV55 S	2		2xNV55 S	5	
7	NV30	1		NV55 S	2		NV55 S	2		2xNV55 S	5	
8	NV35	2		NV55 S	2		NV75 HD	3		2xNV55 S	5	
9	NV35	2		NV55 S	2		NV75 HD	3		2xNV55 S	5	
10	NV35	2		NV55 S	2		2xNV55 S	5		2xNV55 S	5	
11	NV55 S	2		2xNV35	3		2xNV55 S	5		2xNV55 S	5	
12	NV55 S	2		2xNV35	3		2xNV55 S	5		2xNV55 S	5	
13	NV55 S	2		2xNV35	3		2xNV55 S	5		2xNV55 S	5	
14	NV55 S	2		2xNV35	3		2xNV55 S	5		NV110	5	
15	NV55 S	2		2xNV35	3		2xNV55 S	5		NV110	5	
16	2xNV35	3		2xNV55 S	5		NV75 HD	3		NV110	5	
17	2xNV35	3		2xNV55 S	5		NV75 HD	3		NV110	5	
18	2xNV35	3		2xNV55 S	5		NV75 HD	3		NV110	5	
19	2xNV35	3		2xNV55 S	5		NV75 HD	3		NV150	10	
20	2xNV35	3		2xNV55 S	5		NV75 HD	3		NV150	10	
21	2xNV55 S	5					NV110	8		NV150	10	
23	2xNV55 S	5					NV110	8		NV150	10	
24	2xNV55 S	5					NV110	8		NV150	10	
25	2xNV55 S	5					NV110	8		NV150	10	
26										NV150	10	
27										NV150	10	
28										NV150	10	
29										NV150	10	
30										NV150	10	

Ventilatoren

Ringe	NL 11			NL 12			NL 13			NL 14		
[Anzahl]	Typ Ventilator	Anzahl Dachhauben	Anzahl Dachentlüftungsgebläse	Typ Ventilator	Anzahl Dachhauben	Anzahl Dachentlüftungsgebläse	Typ Ventilator	Anzahl Dachhauben	Anzahl Dachentlüftungsgebläse	Typ Ventilator	Anzahl Dachhauben	Anzahl Dachentlüftungsgebläse
1	NV75	6		2xNV55 S	4	1	2xNV75HD	4	1	4xNV55 S	4	1
2	NV75	6		2xNV55 S	4	1	2xNV75HD	4	1	4xNV55 S	4	1
3	NV75	6		2xNV55 S	4	1	2xNV75HD	4	1	4xNV55 S	4	1
4	NV75	6		2xNV55 S	4	1	2xNV75HD	4	1	4xNV55 S	4	1
5	NV75	6		2xNV55 S	4	1	2xNV75HD	4	1	4xNV55 S	4	1
6	NV75	6		2xNV55 S	4	1	2xNV75HD	4	1	4xNV55 S	4	1
7	NV75	6		2xNV55 S	4	1	2xNV75HD	4	1	4xNV55 S	4	1
8	NV75	6		2xNV55 S	4	1	2xNV75HD	4	1	4xNV55 S	4	1
9	NV75	6		2xNV55 S	4	1	2xNV75HD	4	1	4xNV55 S	4	1
10	NV75	6		2xNV55 S	4	1	2xNV75HD	4	1	4xNV55 S	4	1
11	NV75	6		NV110	4	1	NV150	4	1	4xNV55 S	4	1
12	NV75	6		NV110	4	1	NV150	4	1	4xNV55 S	4	1
13	NV75	6		NV110	4	1	NV150	4	1	4xNV55 S	4	1
14	NV110	8		NV110	4	1	NV150	4	1	4xNV55 S	4	1
15	NV110	8		NV110	4	1	NV150	4	1	4xNV55 S	4	1
16	NV110	8		NV150	4	1	NV185	4	1	2xNV110	4	2
17	NV110	8		NV150	4	1	NV185	4	1	2xNV110	4	2
18	NV110	8		NV150	4	1	NV185	4	1	2xNV110	4	2
19	NV110	8		NV150	4	1	NV185	4	1	2xNV110	4	2
20	NV110	8		NV150	4	1	NV185	4	1	2xNV110	4	2
21	NV150	10		NV185	4	2	2xNV110	4	2	2xNV110	4	2
23	NV150	10		NV185	4	2	2xNV110	4	2	2xNV110	4	2
24	NV150	10		NV185	4	2	2xNV110	4	2	2xNV110	4	2
25	NV150	10		NV185	4	2	2xNV110	4	2	2xNV110	4	2
26	NV185	12		2xNV110	4	2				2xNV150	4	2
27	NV185	12		2xNV110	4	2				2xNV150	4	2
28	NV185	12		2xNV110	4	2				2xNV150	4	2
29	NV185	12		2xNV110	4	2				2xNV150	4	2
30	NV185	12		2xNV110	4	2				2xNV150	4	2

Ventilatoren

Ringe	NL 16			NL 18			NL 20			NL 22		
[Anzahl]	Typ Ventilator	Anzahl Dachhauben	Anzahl Dachentlüftungsgebläse	Typ Ventilator	Anzahl Dachhauben	Anzahl Dachentlüftungsgebläse	Typ Ventilator	Anzahl Dachhauben	Anzahl Dachentlüftungsgebläse	Typ Ventilator	Anzahl Dachhauben	Anzahl Dachentlüftungsgebläse
1	4xNV55 S	4	1	4xNV75HD	4	2	2xNV110	5	2	2xNV110	5	3
2	4xNV55 S	4	1	4xNV75HD	4	2	2xNV110	5	2	2xNV110	5	3
3	4xNV55 S	4	1	4xNV75HD	4	2	2xNV110	5	2	2xNV110	5	3
4	4xNV55 S	4	1	4xNV75HD	4	2	2xNV110	5	2	2xNV110	5	3
5	4xNV55 S	4	1	4xNV75HD	4	2	2xNV110	5	2	2xNV110	5	3
6	4xNV55 S	4	1	4xNV75HD	4	2	2xNV110	5	2	2xNV110	5	3
7	4xNV55 S	4	1	4xNV75HD	4	2	2xNV110	5	2	2xNV110	5	3
8	4xNV55 S	4	1	4xNV75HD	4	2	2xNV110	5	2	2xNV110	5	3
9	4xNV55 S	4	1	4xNV75HD	4	2	2xNV110	5	2	2xNV110	5	3
10	4xNV55 S	4	1	4xNV75HD	4	2	2xNV110	5	2	2xNV110	5	3
11	2xNV110	4	2	2xNV110	4	2	2xNV150	5	2	2xNV185	5	3
12	2xNV110	4	2	2xNV110	4	2	2xNV150	5	2	2xNV185	5	3
13	2xNV110	4	2	2xNV110	4	2	2xNV150	5	2	2xNV185	5	3
14	2xNV110	4	2	2xNV110	4	2	2xNV150	5	2	2xNV185	5	3
15	2xNV110	4	2	2xNV110	4	2	2xNV150	5	2	2xNV185	5	3
16	2xNV150	4	2	2xNV185	6	2	NV220+NV185	5	3	2xNV220	8	3
17	2xNV150	4	2	2xNV185	6	2	NV220+NV185	5	3	2xNV220	8	3
18	2xNV150	4	2	2xNV185	6	2	NV220+NV185	5	3	2xNV220	8	3
19	2xNV150	4	2	2xNV185	6	2	NV220+NV185	5	3	2xNV220	8	3
20	2xNV150	4	2	2xNV185	6	2	NV220+NV185	5	3	2xNV220	8	3
21	2xNV185	6	2	4xNV110	6	3	4xNV150	8	4	4xNV150	8	4
23	2xNV185	6	2	4xNV110	6	3	4xNV150	8	4	4xNV150	8	4
24	2xNV185	6	2	4xNV110	6	3	4xNV150	8	4	4xNV150	8	4
25	2xNV185	6	2	4xNV110	6	3	4xNV150	8	4	4xNV150	8	4
26		6	3	4xNV110	6	3	4xNV150	8	4	4xNV185	8	4
27		6	3	4xNV110	6	3	4xNV150	8	4	4xNV185	8	4
28		6	3	4xNV110	6	3	4xNV150	8	4	4xNV185	8	4
29		6	3	4xNV110	6	3	4xNV150	8	4	4xNV185	8	4
30		6	3	4xNV110	6	3	4xNV150	8	4	4xNV185	8	4

Ventilatoren

Ringe [Anzahl]	NLK 2		NLK 3		NLK 4		NLK 5		NLK 6	
	Typ Ventilator	Anzahl Dachhauben	Typ Ventilator	Anzahl Dachhauben	Typ Ventilator	Anzahl Dachhauben	Typ Ventilator	Anzahl Dachhauben	Typ Ventilator	Anzahl Dachhauben
5	NV11	1	NV11	1	NV11	1	NV11	1	NV30	1
6	NV11	1	NV11	1	NV11	1	NV11	1	NV30	1
7	NV11	1	NV11	1	NV11	1	NV11	1	NV30	1
8	NV11	1	NV11	1	NV11	1	NV30	1	NV30	1
9	NV11	1	NV11	1	NV30	1	NV30	1	NV35	2
10	NV11	1	NV11	1	NV30	1	NV30	1	NV35	2
11	NV11	1	NV11	1	NV30	1	NV30	1	NV35	2
12	NV11	1	NV11	1	NV30	1	NV30	1	NV35	2
13	NV11	1	NV11	1	NV30	1	NV30	1	NV35	2
14	NV11	1	NV11	1	NV30	1	NV30	1	NV75 HD	3
15	NV11	1	NV11	1	NV30	1	NV30	1	NV75 HD	3
16	NV11	1	NV11	1	NV30	1	NV35	1	NV75 HD	3
17	NV11	1	NV11	1	NV30	1	NV35	1	NV75 HD	3
18	NV11	1	NV11	1	NV30	1	NV35	1	NV75 HD	3
19	NV11	1	NV11	1			NV75 HD	1	NV75 HD	3
20	NV11	1	NV11	1			NV75 HD	1	NV75 HD	3
21	NV11	1	NV11	1			NV75 HD	1	NV75 HD	3
22	NV11	1	NV11	1			NV75 HD	1	NV75 HD	3
23	NV11	1	NV11	1			NV75 HD	1	NV75 HD	3
24	NV11	1	NV11	1						
25	NV11	1	NV11	1						

Ringe [Anzahl]	NLK 6		NLK 7		NLK 8		NLK 9		NLK 10	
	Typ Ventilator	Anzahl Dachhauben	Typ Ventilator	Anzahl Dachhauben	Typ Ventilator	Anzahl Dachhauben	Typ Ventilator	Anzahl Dachhauben	Typ Ventilator	Anzahl Dachhauben
5	NV30	1	NV30	1	NV35	2	NV55 S	2	2xNV55 S	5
6	NV30	1	NV30	1	NV35	2	NV55 S	2	2xNV55 S	5
7	NV30	1	NV30	1	NV55 S	2	NV55 S	2	2xNV55 S	5
8	NV30	1	NV35	2	NV55 S	2	NV75 HD	3	2xNV55 S	5
9	NV35	2	NV35	2	NV55 S	2	NV75 HD	3	2xNV55 S	5
10	NV35	2	NV35	2	NV55 S	2	NV75 HD	3	2xNV55 S	5
11	NV35	2	NV55 S	2	2xNV35	3	2xNV55 S	5	2xNV55 S	5
12	NV35	2	NV55 S	2	2xNV35	3	2xNV55 S	5	2xNV55 S	5
13	NV35	2	NV55 S	2	2xNV35	3	2xNV55 S	5	2xNV55 S	5
14	NV75 HD	3	NV55 S	2	2xNV35	3	2xNV55 S	5	2xNV55 S	5
15	NV75 HD	3	NV55 S	2	2xNV35	3	2xNV55 S	5	2xNV55 S	5
16	NV75 HD	3	2xNV35	3	2xNV55 S	5	2xNV75 S	5	NV110	5
17	NV75 HD	3	2xNV35	3	2xNV55 S	5	2xNV75 S	5	NV110	5
18	NV75 HD	3	2xNV35	3	2xNV55 S	5	2xNV75 S	5	NV110	5
19	NV75 HD	3	2xNV35	3	2xNV55 S	5	2xNV75 S	5	NV110	5
20	NV75 HD	3	2xNV35	3	2xNV55 S	5	2xNV75 S	5	NV110	5
21	NV75 HD	3	2xNV55 S	5			NV110	8		
22	NV75 HD	3	2xNV55 S	5			NV110	8		
23	NV75 HD	3	2xNV55 S	5			NV110	8		

Ringe [Anzahl]	NLI 2 Typ Ventilator	NLI 3 Typ Ventilator	NLI 4 Typ Ventilator	NLI 5 Typ Ventilator	NLI 6 Typ Ventilator	NLI 7 Typ Ventilator
1	NV11	NV11	NV11	NV11	NV30	NV30
2	NV11	NV11	NV11	NV11	NV30	NV30
3	NV11	NV11	NV11	NV11	NV30	NV30
4	NV11	NV11	NV11	NV11	NV30	NV30
5	NV11	NV11	NV11	NV11	NV30	NV30
6	NV11	NV11	NV11	NV11	NV30	NV30
7	NV11	NV11	NV11	NV11	NV30	NV30
8	NV11	NV11	NV11	NV30	NV30	NV35
9	NV11	NV11	NV30	NV30	NV30	NV35
10	NV11	NV11	NV30	NV30	NV30	NV35

Ringe [Anzahl]	NLT 2 Typ Ventilator	NLT 3 Typ Ventilator	NLT 4 Typ Ventilator	NLT 5 Typ Ventilator	NLT 6 Typ Ventilator	NLT 7 Typ Ventilator
1	NV11	NV11	NV11	NV11	NV30	NV30
2	NV11	NV11	NV11	NV11	NV30	NV30
3	NV11	NV11	NV11	NV11	NV30	NV30
4	NV11	NV11	NV11	NV11	NV30	NV30
5	NV11	NV11	NV11	NV11	NV30	NV30
6	NV11	NV11	NV11	NV11	NV30	NV30
7	NV11	NV11	NV11	NV30	NV30	NV30
8	NV11	NV11	NV11	NV30	NV30	NV35
9	NV11	NV30	NV30	NV30	NV30	NV35
10	NV11	NV30	NV30		NV30	NV35
11	NV11	NV30	NV30			
12	NV11	NV30	NV30			

Zuordnung von Ventilatoren - Empfehlung

Silotyp			Typ Ventilator	Anzahl Dachhauben	Anzahl Dachentlüftungsgebläse
NLK 2	-	NLK 3	**NV 11**	1	
NLK 4/5	-	NLK 4/10	**NV 11**	1	
NLK 4/11	-	NLK 4/20	**NV 30**	1	
NLK 5/5	-	NLK 5/7	**NV 11**	1	
NLK 5/8	-	NLK 5/15	**NV 30**	1	
NLK 5/16	-	NLK 5/20	**NV 35**	1	
NLK 5/21	-	NLK 5/23	**NV 75 HD**	1	
NLK 6/5	-	NLK 6/10	**NV 30**	1	
NLK 6/11	-	NLK 6/15	**NV 35**	**2**	
NLK 6/16	-	NLK 6/23	**NV 75 HD**	**3**	
NLK 7/5	-	NLK 7/7	**NV 30**	**1**	
NLK 7/8	-	NLK 7/10	**NV 35**	**2**	
NLK 7/11	-	NLK 7/15	**NV 55 S**	**2**	
NLK 7/16	-	NLK 7/20	**2 x NV 35**	**3**	
NLK 7/21	-	NLK 7/23	**2 x NV 55 S**	**5**	
NLK 8/5	-	NLK 8/6	**NV 35**	2	
NLK 8/7	-	NLK 8/10	**NV 55 S**	2	
NLK 8/11	-	NLK 8/15	**2 x NV 35**	3	
NLK 8/16	-	NLK 8/20	**2 x NV 55 S**	5	
NLK 9/5	-	NLK 9/7	**NV 55 S**	2	
NLK 9/8	-	NLK 9/10	**NV 75 HD**	3	
NLK 9/11	-	NLK 9/15	**2 x NV 55 S**	5	
NLK 9/16	-	NLK 9/20	**2 x NV 75 HD**	5	
NLK 9/21	-	NLK 9/23	**NV 110**	8	
NLK 10/7	-	NLK 10/15	**2 x NV 55 S**	5	
NLK 10/16	-	NLK 10/20	**NV 110**	5	

Zuordnung von Ventilatoren - Empfehlung

Silotyp			Typ Ventilator
NLI 2	-	NLI 3	**NV 11**
NLI 4/5	-	NLI 4/10	**NV 11**
NLI 4/11	-	NLI 4/20	**NV 30**
NLI 5/5	-	NLI 5/7	**NV 11**
NLI 5/8	-	NLI 5/15	**NV 30**
NLI 5/16	-	NLI 5/20	**NV 35**
NLI 5/21	-	NLI 5/25	**NV 75 HD**
NLI 6/5	-	NLI 6/10	**NV 30**
NLI 6/11	-	NLI 6/15	**NV 35**
NLI 6/16	-	NLI 6/25	**NV 75 HD**
NLI 7/5	-	NLI 7/7	**NV 30**
NLI 7/8	-	NLI 7/10	**NV 35**

Zuordnung von Ventilatoren - Empfehlung

Silotyp			Typ Ventilator
NLT 2	-	NLT 3/8	NV 11
NLT 3/9	-	NLT 3/15	NV 30
NLT 4/1	-	NLT 4/8	NV 11
NLT 4/9	-	NLT 4/12	NV 30
NLT 5/1	-	NLT 5/6	NV 11
NLT 5/7	-	NLT 5/9	NV30

Zuordnung von Ventilatoren - Empfehlung

Silotyp			Typ Ventilator	Anzahl Dachhauben	Anzahl Dachentlüftungsgebläse
NL 2	-	NL 3	**NV 11**	1	
NL 4/5	-	NL 4/10	**NV 11**	1	
NL 4/11	-	NL 4/20	**NV 30**	1	
NL 5/5	-	NL 5/7	**NV 11**	1	
NL 5/8	-	NL 5/15	**NV 30**	1	
NL 5/16	-	NL 5/20	**NV 35**	1	
NL 5/21	-	NL 5/25	**NV 75 HD**	1	
NL 6/5	-	NL 6/10	**NV 30**	1	
NL 6/11	-	NL 6/15	**NV 35**	**2**	
NL 6/16	-	NL 6/25	**NV 75 HD**	**3**	
NL 7/5	-	NL 7/7	**NV 30**	**1**	
NL 7/8	-	NL 7/10	**NV 35**	**2**	
NL 7/11	-	NL 7/15	**NV 55 S**	**2**	
NL 7/16	-	NL 7/20	**2 x NV 35**	**3**	
NL 7/21	-	NL 7/25	**2 x NV 55 S**	**5**	
NL 8/5	-	NL 8/6	**NV 35**	2	
NL 8/7	-	NL 8/10	**NV 55 S**	2	
NL 8/11	-	NL 8/15	**2 x NV 35**	3	
NL 8/16	-	NL 8/20	**2 x NV 55 S**	5	
NL 9/5	-	NL 9/7	**NV 55 S**	2	
NL 9/8	-	NL 9/10	**NV 75 HD**	3	
NL 9/11	-	NL 9/15	**2 x NV 55 S**	5	
NL 9/16	-	NL 9/20	**2 x NV 75 HD**	5	
NL 9/21	-	NL 9/25	**NV 110**	8	
NL 10/7	-	NL 10/15	**2 x NV 55 S**	5	
NL 10/16	-	NL 10/20	**NV 110**	5	
NL 10/21	-	NL 10/30	**NV 150**	10	
NL 11/7	-	NL 11/15	**NV 75**	6	
NL 11/16	-	NL 11/20	**NV 110**	8	
NL 11/21	-	NL 11/25	**NV 150**	10	
NL 11/26	-	NL 11/30	**NV 185**	12	
NL 12/7	-	NL 12/10	**2 x NV 55 S**	4	1
NL 12/11	-	NL 12/15	**NV 110**	4	1
NL 12/16	-	NL 12/20	**NV 150**	4	1
NL 12/21	-	NL 12/25	**NV 185**	4	2
NL 12/26	-	NL 12/30	**2 x NV 110**	4	2
NL 13/7	-	NL 13/10	**2 x NV 75 HD**	4	1
NL 13/11	-	NL 13/15	**NV 150**	4	1
NL 13/16	-	NL 13/20	**NV 185**	4	1
NL 13/21	-	NL 13/25	**2 x NV 110**	4	2
NL 14/7	-	NL 14/15	**4 x NV 55 S**	4	1
NL 14/16	-	NL 14/25	**2 x NV 110**	4	2
NL 14/26	-	NL 14/30	**2 x NV 150**	4	2
NL 16/7	-	NL 16/10	**4 x NV 55 S**	4	1
NL 16/11	-	NL 16/15	**2 x NV 110**	4	2
NL 16/16	-	NL 16/20	**2 x NV 150**	4	2
NL 16/21	-	NL 16/25	**2 x NV 185**	6	2
NL 16/26	-	NL 16/30	**NV 220 + NV 185**	6	3
NL 18/7	-	NL 18/10	**4 x NV 75 HD**	4	2
NL 18/11	-	NL 18/15	**2 x NV 110**	4	2
NL 18/16	-	NL 18/20	**2 x NV 185**	6	2
NL 18/21	-	NL 18/30	**4 x NV 110**	6	3
NL 20/7	-	NL 20/10	**2 x NV 110**	5	2
NL 20/11	-	NL 20/15	**2 x NV 150**	5	2
NL 20/16	-	NL 20/20	**NV 220 + NV 185**	5	3
NL 20/21	-	NL 20/30	**4 X NV 150**	8	4
NL 22/7	-	NL 22/10	**2 x NV 110**	5	3
NL 22/11	-	NL 22/15	**2 x NV 185**	5	3
NL 22/16	-	NL 22/20	**2 x NV 220**	8	3
NL 22/21	-	NL 22/25	**4 x NV 150**	8	4
NL 22/26	-	NL 22/30	**4 x NV 185**	8	4

S-Serie | mobile Restentleerung


S-Serie


Transportable mobile Fegeschnecke zur Restentleerung Typ NFR


Für kleine und mittelgroße landwirtschaftliche Betriebe hat NEUERO den Fegeschneckentyp NFR entwickelt. Die Fegeschnecke eine zuverlässige und leistungsstarke Möglichkeit zur Restentleerung von Getreide aus den Flachboden Silos Typ NL. Sie startet, wenn die mechanische Entleerung des Silos endet und trägt die Restmenge durch 360° Drehung aus. Die Fegeschnecke ist lieferbar für Flachboden Silos bis zum Durchmesser von 9,83 m und in den Leistungsklassen 15 t/h und 30 t/h. Für den ruhigen Antrieb wird die Fegeschnecke mit Getriebemotor geliefert.


Merkmale:
- Leistungsklassen: 15 t/h und 30 t/h
- Komplett mit Getriebemotor, Gelenkzapfen, Fegeschneckenkreuz und Lauf- und Führungsrad
- Verstärkte Schneckenseele, dadurch geringe Wartung, lange Lebensdauer
- Transportable mobile Fegeschnecken zum Umsetzen in Silos mit gleichem Durchmesser
- Flexibel und wirtschaftlich einsetzbar

Fegeschnecken zur Restentleerung für Getreide, transportabel, komplett mit Getriebemotor, verwendbar für mehrere Silos gleichen Durchmessers				**NFR 15 für Leistung bis 15 t/h**	**NFR 30 für Leistung bis 30 t/h**
Silotyp	**Silo-Ø**	**Schneckenlänge m**	**Motor kW**	**Art.-Nr.**	**Art.-Nr.**
NL 4	3,58	1,50	1,5	4440100	4440300
NL 5	4,47	2,00	1,5	4440110	4440310
NL 6	5,36	2,50	1,5	4440120	4440320
NL 7	6,26	3,00	2,2	4440130	4440330
NL 8	7,15	3,25	2,2	4440140	4440340
NL 9	8,04	3,75	2,2	4440150	4440350
NL 10	8,94	4,25	2,2	4440160	-
NL 10	8,94	4,25	3,0	-	4440360
NL 11	9,83	4,75	3,0	4440165	4440365
Zubehör				**Art.-Nr.**	**Art.-Nr.**
Stützdach für NL 4				4441000	4441000
Stützdach für NL 5				4441010	4441010
Stützdach für NL 6				4441020	4441020
Stützdach für NL 7				4441030	4441030
Stützdach für NL 8				4441040	4441040
Stützdach für NL 9				4441050	4441050
Stützdach für NL 10				4441060	4441060
Aufnahmekreuz für Fegeschnecke Restentleerung				4440060	4440060
Rahmen mit Aufnahmekreuz				4440070	4440070

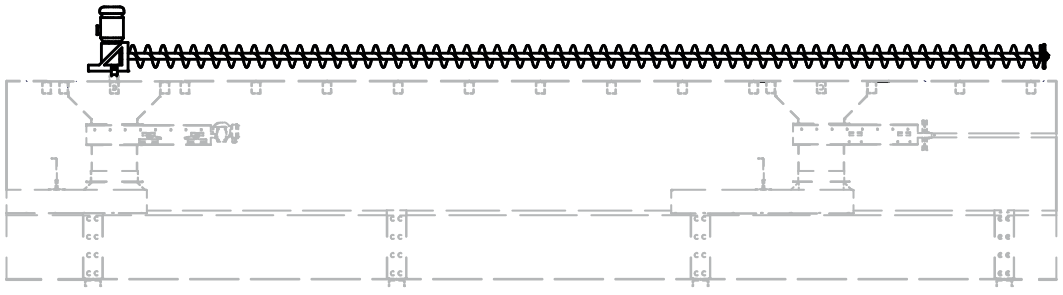

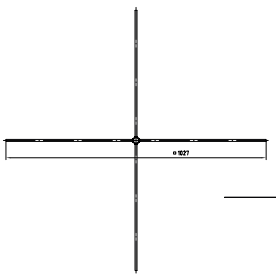

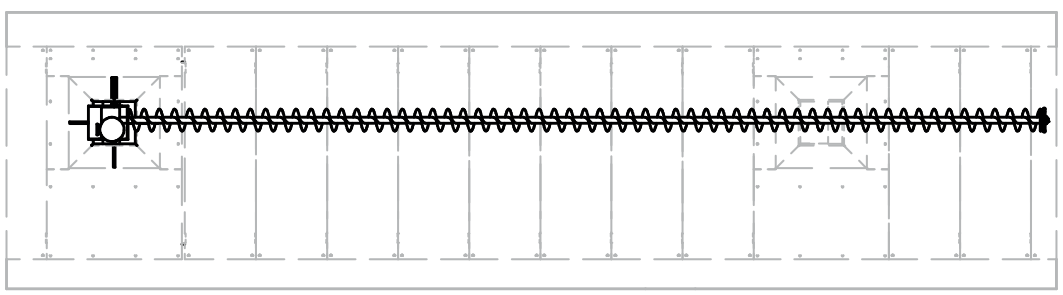

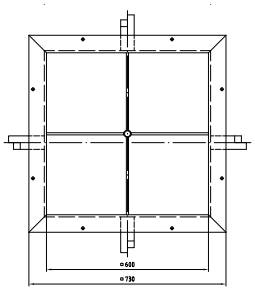

L-Serie | stationäre Restentleerung


L-Serie


Stationäre Fegeschnecke zur Restentleerung vom Typ NFS


Für landwirtschaftliche Betriebe mit einem Leistungsanspruch von 25 t/h, 40 t/h oder 60 t/h hat NEUERO den Typ NFS entwickelt. Die Fegeschnecke ist ein leichtes stationäres Gerät zur Restentleerung von Getreide aus Flachboden Silos des Typs NL 6 bis 8. Die Fegeschnecke wurde speziell für den landwirtschaftlichen Einsatz ausgerüstet, zeichnen sich durch ihre modulare Bauweise aus und lässt sich lastabhängig steuern.


Merkmale:
- Leichter Einbau und einfache Bedienung
- Lieferumfang: verstärkte Schneckenseele, Getriebemotor, Gelenkzapfen, Fegeschneckenkreuz, Lauf- und Führungsrad sowie Drehkollektor
- Lastabhängiger Antrieb für die gleichmäßige Entleerung und Vermeidung von Unterfahren des Getreidestapels
- Automatischer Vorschub 360°
- auf Wunsch nach der ATEX-Richtlinie lieferbar

Typ Leistung	NFS 25 Förderleistung 25 t/h		NFS 40 Förderleistung 40 t/h	
Silotyp	**Antriebsleistung [kW]**	**Art.-Nr**	**Antriebsleistung [kW]**	**Art.-Nr**
NL6	2,2	4442000	3,0	4442100
NL7	2,2	4442010	3,0	4442110
NL8	2,2	4442020	3,0	4442120

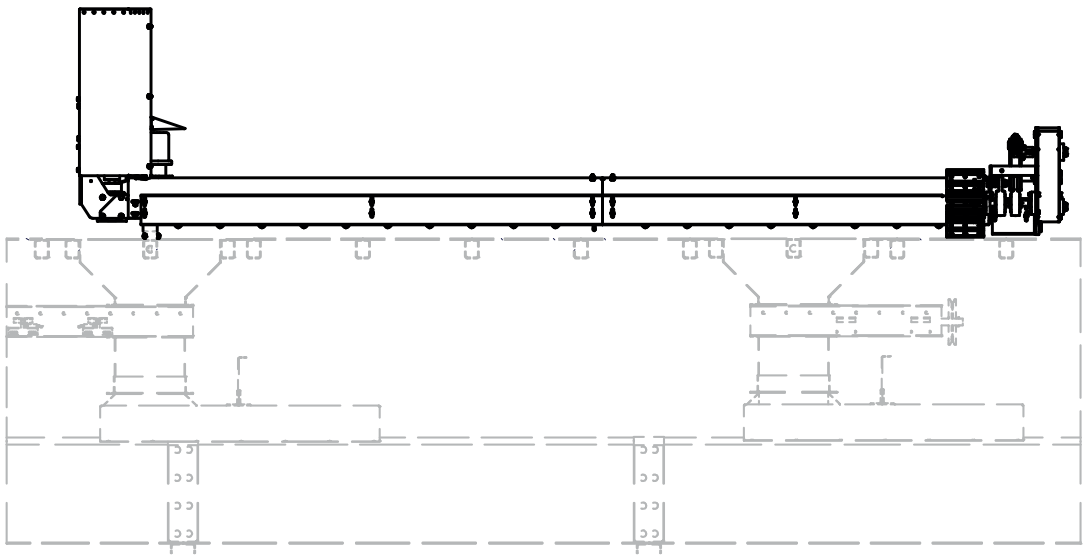

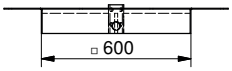

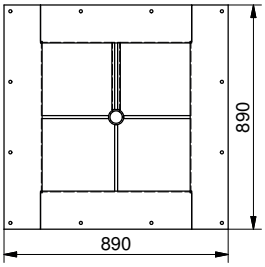

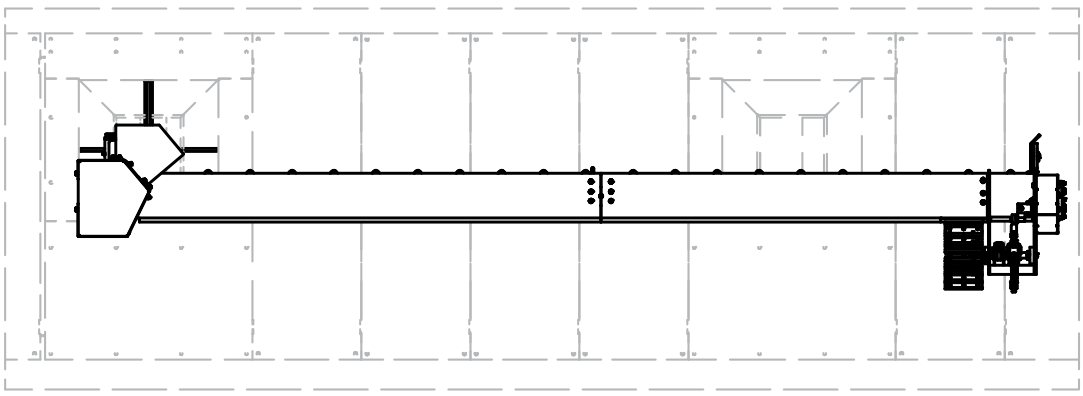


HD-Serie

Stationäre Fegeschnecke zur Restentleerung vom Typ NFS

Für anspruchsvolle Anwendungen auf landwirtschaftlichen Betrieben oder in Umschlagslägern hat NEUERO die Fegeschnecke des Typs NFS entwickelt. Die Fegeschnecke deckt die Leistungsanforderungen von 40 t/h bis 100 t/h ab. Sie wird eingebaut in Flachboden Silos von NEUERO des Typs NL 6 bis NL 32.
Die Fegeschnecke NFS wird sowohl mit einem Schneckenantrieb am Fegeschneckenkreuz sowie mit einem Antrieb für das Lauf- und Führungsrad ausgeliefert.

Merkmale


leichter Einbau und einfache Bedienung
Lieferumfang: verstärkte Scheckenseele, Zwischenlagerung, Getriebmotor für Schenckenantrieb, Gelenkzapten, Fegeschneckenkreuz, Lauf- und Führungsrad sowie Drehkollektor
Lastabhängiger Antrieb für die gleichmäßige Entleerung und Vermeidung von Unterfahren des Getreidestapels
Automatischer Vorschub 360°
auf Wunsch nach der ATEX-Richtlinie lieferbar

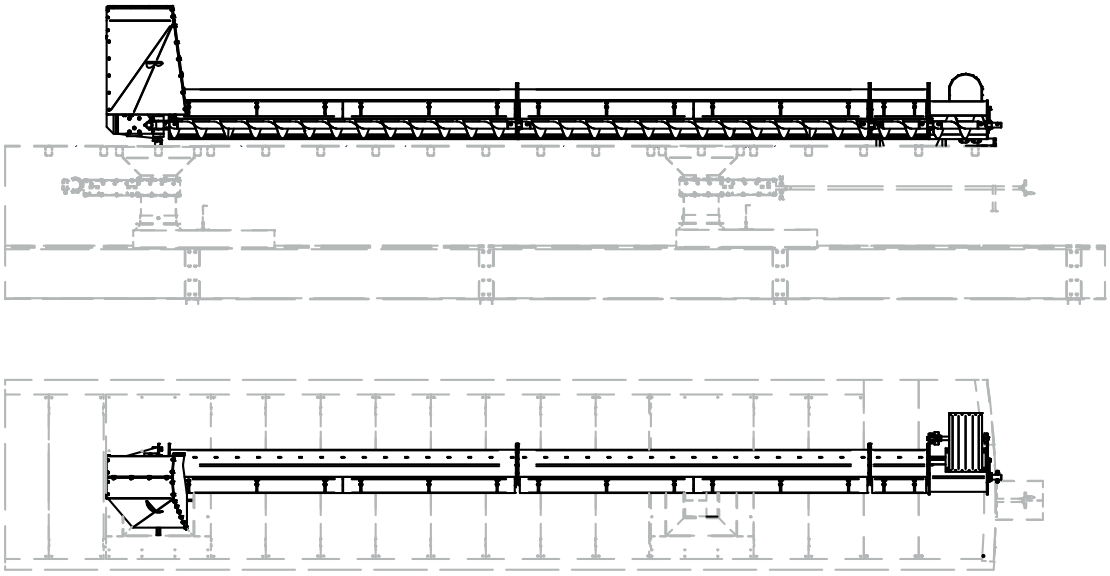

Hinweis
In Silos darf nur mit Erlaubnis des Aufsichtsführenden und in Gegenwart einer Beobachtungsperson eingestiegen werden. Während des Betriebes von Fegeschnecken ist das Betreten generell verboten. Beim Verwenden einer Siloeinstiegstür sollte ein Sicherheitsschalter installiert werden.

Aufteilung der Fegeschneckensegmente NFS HD 40, 60, 80, 100


Silotyp NL	Silodurch-messer	Radius	Grundlänge der Antriebs-träger	Zwischenträger				Vorschub	Endträger	gewünschter Abstand von der Silowand	Tatsächlicher Abstand von der Silowand
								505		80	
6	5363	2681	1966						115		95
7	6257	3128	1966	500					0		157
8	7151	3575	2966						0		104
9	8044	4022	2966	500					0		51
10	8938	4469	2966	500					300		198
11	9832	4916	2966	1000					300		145
12	10726	5363	2966	1500					300		92
13	11620	5810	2966	2000					200		139
14	12513	6257	2966	2500					200		86
16	14301	7151	2966	3000	500				0		180
18	16089	8044	2966	3000	1500				0		73
20	17876	8938	2966	3000	2000				300		167
22	19664	9832	2966	3000	3000				200		161
24	21452	10726	2966	3000	3000	1000			115		140
27	24133	12066	2966	3000	3000	2500			0		95
30	26814	13407	2966	3000	3000	3000	500		300		136
32	28602	14301	2966	3000	3000	3000	1500		200		130

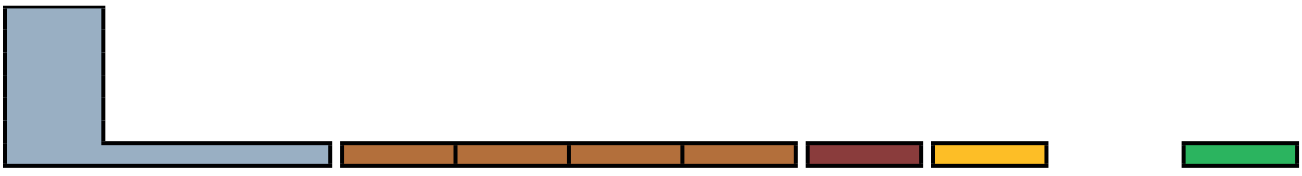


Steigleiter mit Rückenschutz


Steigleiter mit Rückenschutz mit Podest					
Steigleiter für Typ			NL		NLT
Anzahl der Ringe	Länge m	Anzahl der Ruhepodeste	Art.-Nr.	Anzahl der Ruhepodeste	Art.-Nr.
2	-	-	-	-	3417500
3	-	-	-	-	3417600
4	-	-	-	-	3417700
5	2,5	-	3417500	-	3417800
6	3,4	-	3417600	-	3417900
7	4,2	-	3417700	-	3418000
8	5,0	-	3417800	-	3418100
9	5,9	-	3417900	1	3418201
10	6,7	-	3418000	1	3418301
11	7,6	-	3418100	1	3418401
12	8,4	1	3418201	1	3418501
13	9,3	1	3418301	2	3418602
14	10,1	1	3418401	2	3418702
15	11,0	1	3418501	2	3418802
16	11,8	2	3418602	2	-
17	12,6	2	3418702	2	-
18	13,5	2	3418802	2	-
19	14,3	2	3418902	2	-
20	15,1	2	3419002	2	-
21	16,0	2	3419102	2	-
22	16,8	3	3419203	3	-
					Art.-Nr.
Zwischen- und Ruhepodeste für Steigleitern über 10 m Lauflänge alle 6 m erforderlich (Vorschrift Berufsgenossenschaft)					3420000

Zubehör		NL6/9	NL7/9	NL8/9	NL9/9	NL10/9	NL11/9	NL12/9	NL14/9	NL16/9
Treppe (rechtsgängig)	Art.-Nr.	3092005	3092010	3092015	3092020	3092025	3092030	3092035	3092040	3092045

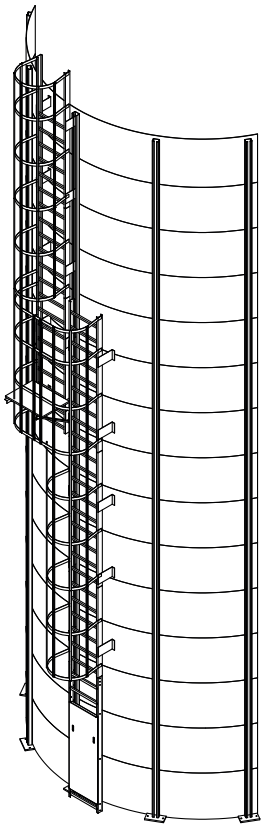

Steigleiter mit Rückenschutz

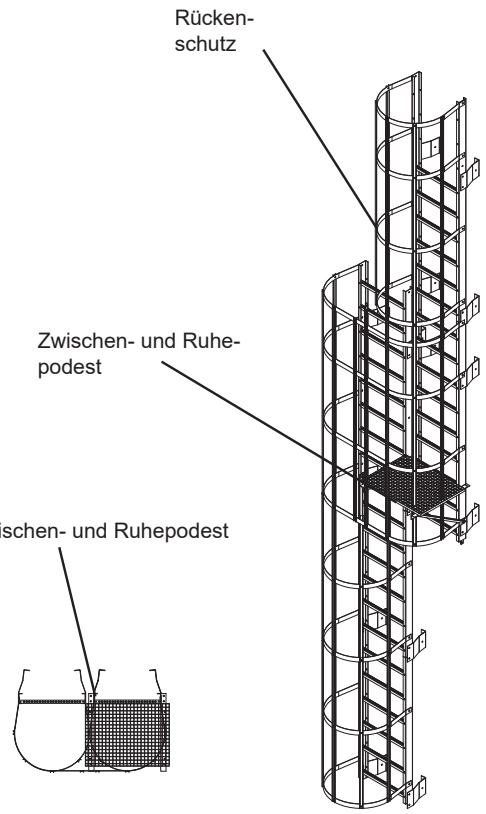

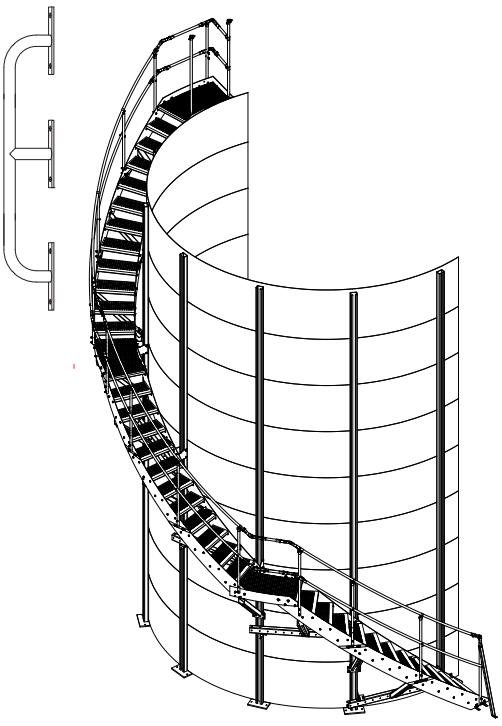


Aufstiegstreppe


Silolaufsteg

Silolaufsteg und Trogkettenförderer-Brücke	Art.-Nr.
Laufsteg (schmal) in verzinkter Stahlkonstruktion (geschraubte Ausführung), mit Geländer, Laufstegbreite innen 0,85 m, Laufstegbreite außen 1,00 m, Laufsteghöhe = 1,1 m, Lauffläche = 2/3 mit Gitterrosten ausgelegt, pro 1,8 m	-
Laufsteg (breit) in verzinkter Stahlkonstruktion (geschraubte Ausführung), mit Geländer, Laufstegbreite innen 1,1 m, Laufstegbreite außen 1,26 m, Laufsteghöhe = 1,1 m, Lauffläche = 2/3 mit Gitterrosten ausgelegt, pro 1,8 m	-
Roste schmal, 425 mm x 1,685 mm, verzinkt (für volle Auslegung)	0042640
Roste breit, 685 mm x 1,685 mm, verzinkt	0043563
Laufsteg-Auflage in verzinkter und geschraubter Ausführung für Doppelstützenanschluss einschl. Stützenschuhe und Stützen	
für NL 5 pro Stück	2870380
für NL 6 pro Stück	2870390
für NL 7 pro Stück	2870400
für NL 8 pro Stück	2870410
für NL 9 pro Stück	2870420
für NL 10 pro Stück	2870430
für NL 11 pro Stück	2870440
Zwischen- und Ruhepodest (bei Steigleitern über 10 m Lauflänge alle 6 m erforderlich)	3420000
Torbogen zur Laufstegverbindung mit einem Geländerdurchbruch	3420050
Zwickelpodest f. Siloabstand 0,5 - 1,2 m mit Geländer	3420100
Zwickelpodest f. Siloabstand 1,2 - 1,5 m mit Geländer	3420115
Winkel mit Klemmstück	2851600
Arbeitsbühne für NL-Silo	3420260


Laufsteg (schmal)

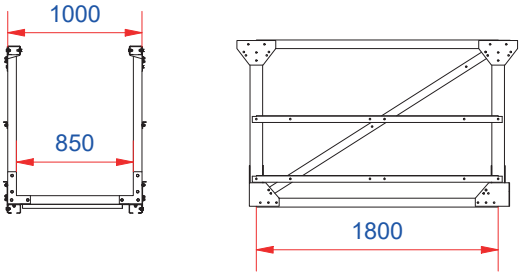


Laufsteg (breit)

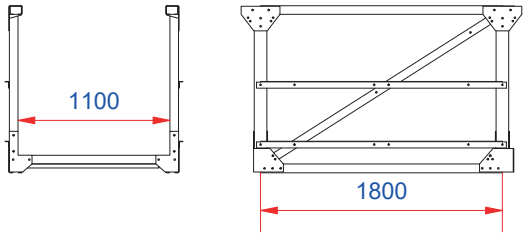



Auflage Fördertechnik	Art.-Nr.
Auflage Fördertechnik TS/NRL NL5	5501600
Auflage Fördertechnik TS/NRL NL6	5501601
Auflage Fördertechnik TS/NRL NL7	5501602
Auflage Fördertechnik TS/NRL NL8	5501603
Auflage Fördertechnik TS/NRL NL9	5501604
Auflage Fördertechnik TS/NRL NL10	5501605

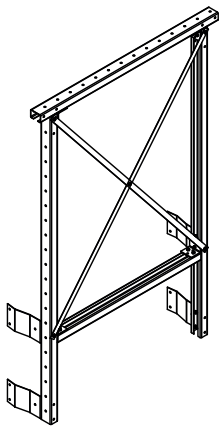



Silolaufsteg

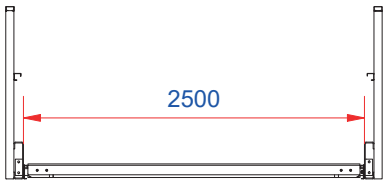


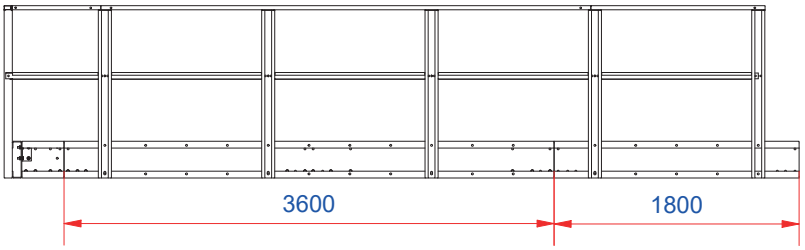

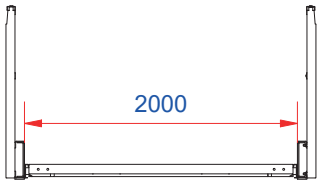

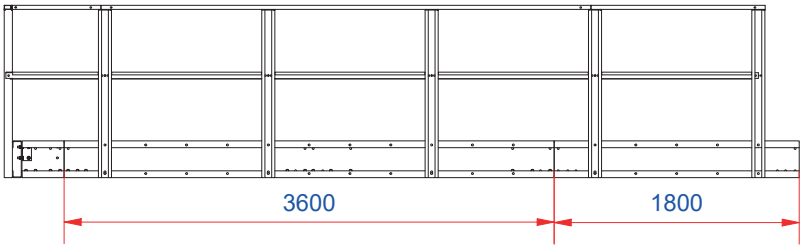

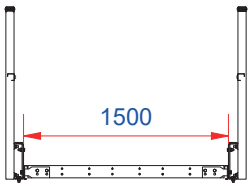


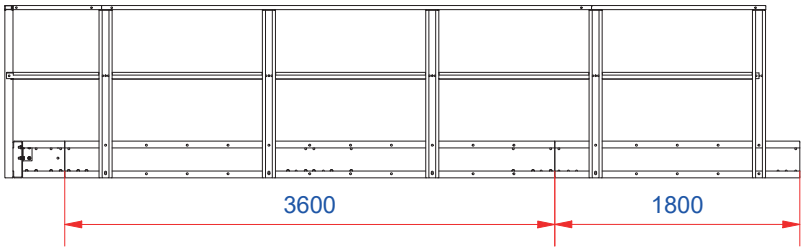

Temperaturmesssystem

iGrain	Ar.Nr.
Handgerät 2000 mit Koffer	4100057
Handgerät 2500 mit Koffer	4100058
Steckdose Handgerät 1m Kabel	4100059
Sicherheitsbarriere ATEX	4100060
Befestigung Temperaturmessgehänge Dach	4100061
Kontrollsystem Wandschrank	4100062
Signalschnittstelle SUB-HUB	4100065
Master HUB 220 V	4100055
Temperaturmessgehänge 5,5 m 3 Sensoren	4100000
Temperaturmessgehänge 6,5 m 4 Sensoren	4100001
Temperaturmessgehänge 7,5 m 4 Sensoren	4100002
Temperaturmessgehänge 8,5 m 5 Sensoren	4100003
Temperaturmessgehänge 9,5 m 5 Sensoren	4100004
Temperaturmessgehänge 10,5 m 6 Sensoren	4100005
Temperaturmessgehänge 11,5 m 6 Sensoren	4100006
Temperaturmessgehänge 12,5 m 7 Sensoren	4100007
Temperaturmessgehänge 13,5 m 7 Sensoren	4100008
Temperaturmessgehänge 14,5 m 8 Sensoren	4100009
Temperaturmessgehänge 15,5 m 8 Sensoren	4100010
Temperaturmessgehänge 16,5 m 9 Sensoren	4100011
Temperaturmessgehänge 17,5 m 9 Sensoren	4100012
Temperaturmessgehänge 18,5 m 10 Sensoren	4100013
Temperaturmessgehänge 19,5 m 10 Sensoren	4100014
Temperaturmessgehänge 20,5 m 11 Sensoren	4100015
Feuchtigkeits- und Temperaturmessgehänge 5,5 m Sensoren 3/1	4100016
Feuchtigkeits- und Temperaturmessgehänge 6,5 m Sensoren 4/1	4100017
Feuchtigkeits- und Temperaturmessgehänge 7,5 m Sensoren 4/1	4100018
Feuchtigkeits- und Temperaturmessgehänge 8,5 m Sensoren 5/1	4100019
Feuchtigkeits- und Temperaturmessgehänge 9,5 m Sensoren 5/1	4100020
Feuchtigkeits- und Temperaturmessgehänge 10,5 m Sensoren 6/1	4100021
Feuchtigkeits- und Temperaturmessgehänge 11,5 m Sensoren 6/1	4100022
Feuchtigkeits- und Temperaturmessgehänge 12,5 m Sensoren 7/2	4100023
Feuchtigkeits- und Temperaturmessgehänge 13,5 m Sensoren 7/2	4100024
Feuchtigkeits- und Temperaturmessgehänge 14,5m Sensoren 8/2	4100025
Feuchtigkeits- und Temperaturmessgehänge 15,5 m Sensoren 8/2	4100026
Feuchtigkeits- und Temperaturmessgehänge 16,5 m Sensoren 9/2	4100027
Feuchtigkeits- und Temperaturmessgehänge 17,5 m Sensoren 9/2	4100028
Feuchtigkeits- und Temperaturmessgehänge 18,5 m Sensoren 10/2	4100029
Feuchtigkeits- und Temperaturmessgehänge 19,5 m Sensoren 10/2	4100030
Feuchtigkeits- und Temperaturmessgehänge 20,5 m Sensoren 11/2	4100031
CO^2 HUB	4100056
CO^2 Sniffer, Länge 4,0m	4100050
CO^2 Sniffer, Länge 6,0m	4100051
CO^2 Sniffer, Länge 8,0m	4100052
CO^2 Sniffer, Länge 10,0m	4100053
CO^2 Sniffer, Länge 12,0m	4100054
Temperaturmesslanze 1,2m 2 Sens	4100070
Temperaturmesslanze 2,4m 2 Sens	4100071
Installationskabel für Temperaturmessanlage in m (PE = 100)	7009107

Dachverstärkung - Bitte beachten: Beim Einbau eines Temperaturmeßsystems in NL-Silos ist eine Dachverstärkung erforderlich.	**Art.-Nr.**
Dachverstärkung f. NL 4	4870000
Dachverstärkung f. NL 5	4870100
Dachverstärkung f. NL 6	4870200
Dachverstärkung f. NL 7	4870250
Dachverstärkung f. NL 8	4870300
Dachverstärkung f. NL 9	4870450
Dachverstärkung f. NL 9 ab 26 Ringe	4870460
Dachverstärkung f. NL 10	4870500
Dachverstärkung f. NL 10 ab 22 Ringe	4870510
Dachverstärkung f. NL 11	4870600
Dachverstärkung f. NL 11 ab 19 Ringe	4870610

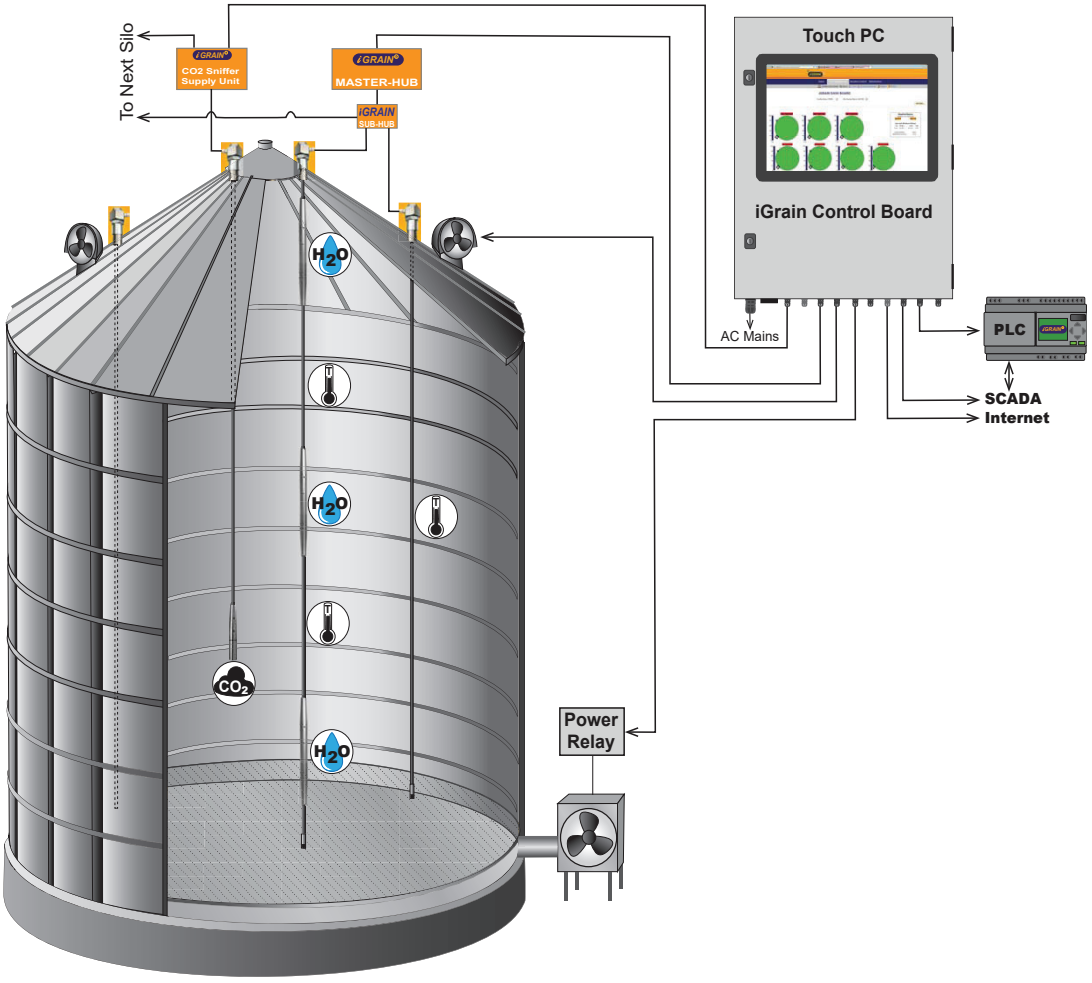

Automatic Exhaust Fan Control

Automatic Aeration Control